新竹縣竹北市公所
清潔隊工作場所改善工程



位置圖

施工說明: 壹、投標前注意事項:

1、本工程之工項及數量，係依總價承包的方式發包，承包廠商於投標前應至現場詳細勘查，並依工程項目及內容詳細估算，
　得自行調整於單價中；得標之廠商得於訂約時，依總金額不變更之原則，調整單價於契約中。
2、本工程承包廠商承攬前即施工前應至現場勘查，施工動線、施工時間與工項須依照學校作息時間，提出施工計畫審核許
　可後方可施工。
3、工程圖書及標單標示之詳圖、規範、廠牌名稱或出產地，為參考資料，均可使用同級品；本工程圖說或標單所註建材規
　格形式或參考廠商，係為本工程使用材料等級，承包廠商得使用同等品，但應提出符合與規範及圖說相符之正式測試報
　告，材料形式，品質與單價比較表，經監造單位及業主審查辦理。
4、圖樣包括本合約所附之施工圖及一切經監造單位及業主核准之各項補充圖樣。
5、圖樣及施工說明書均係說明施工上一切施工程序，構造方法及使用材料規格之重要文件，兩者均有同等效力，其有載明
　於此而未載明於彼，或兩者所載偶有不符者，承包廠商均應遵循監造單位解釋辦理。
6、所有圖樣應以註明尺寸為準，不得以比例尺丈量或由電腦圖中直接取得，數字有錯誤不符或圖樣不明瞭，應即請監造單
　位調整，承包廠商須將各項細部放出足尺大樣，請監造單位核閱認可後，方能施工。
7、設計單位完全之所有圖樣、模型、施工說明書及其副本之版權均屬業主所有。除合約另有規定外，承包廠商均不得使用於
　其他工程，並於工程完工後，若業主要求，應歸還設計單位與業主。

索　引　表

A1－01	索引表　施工圖　施工說明	A3－01	木作詳圖－1
A1－02	施工說明　施工告示牌	A3－02	木作詳圖－2
A2－01	位置圖　地籍圖　地籍套繪圖	A3－03	木作詳圖－3
A2－02	基地配置圖	A3－04	木作詳圖－4
A2－03	原始照核准地上一層平面圖	A3－05	木作詳圖－5
A2－04	地上一層平面圖　天花板　剖立面圖	A3－06	木作詳圖－6
A2－05	門窗圖　大樣圖　無障礙建築專章檢討	A3－07	木作詳圖－7
A2－06	大廳及女性休息區拆除平面圖	A3－08	木作詳圖－8
A2－07	大廳及女性休息區原況圖	A3－09	木作詳圖－9
A2－08	大廳及女性休息區平面配置圖	A3－10	木作詳圖－10
A2－09	大廳及女性休息區平面尺寸圖	A3－11	圍籬詳圖
A2－10	大廳及女性休息區間隔牆配置圖	A3－12	鋁包版入口雨遮
A2－11	大廳及女性休息區地坪配置圖	A3－13	雨遮詳圖
A2－12	大廳及女性休息區天花板圖	A3－14	外觀立面招牌尺寸圖
A2－13	大廳及女性休息區燈具迴路圖		
A2－14	大廳及女性休息區插座配置圖		
A2－15	清潔隊辦公室平面圖		
A2－16	戶外立面圖		

本案施作位置：
30272 新竹縣竹北市成功八路一號

貳、其他工程及施工品管計畫

1、工程告示牌含於假設及雜項工程，不另列項目計價與計量。
2、施工單位應按進度提施工計畫，施工製造圖，品管計畫，經監造單位核准後方得施工。
3、承包廠商應執行安全防護措式，控管工地四周人員安全。
4、注意人員安全，建材不得任意堆置妨礙交通，建築工地須做安全防護，不得讓非工程人員進入。
5、以上費用均含於職業安全衛生、假設及雜項工程，品質管制計畫中。

參、施工大樣圖及樣品

1、施工大樣圖係圖樣，圖表，圖解，說明，性能圖表，手冊，型錄。樣品係材料，設備等之成品及展示匠意之實作。
2、承包廠商應於施工前繪製大樣圖並詳細審閱提送之施工大樣圖及樣品，於施工前10天送審，廠商經監造單位充分時間審查及承包廠商有足夠時間修正，而不致影響工程之進行。
3、施工大樣圖及樣品與合約有不符處，承包廠商應事先提出，否則經監造單位核准，承包廠商仍需負責。
4、承包廠商應將監造單位核覆不合之施工大樣圖及樣品迅予修正後再提送，直至核准為止。監造單位核准之施工大樣圖及樣品均應提送3份。

曾瑞宏

張　號	
圖名	新竹縣竹北市公所清潔隊工作場所改善工程
索引表／施工圖／施工說明	
繪　圖	
設　計	
修　正	
校　對	
日　期	2025-06-30

尚強技術顧問有限公司
台中沙鹿區台灣大道六段1059號

比例尺

圖　號
A1－01

肆、材料及同等品

1、本工程所採用之材料於進場施工前，需附原廠出廠或進口證明書及其他應附之證明文件，經監造單位核可後方得施工。
2、本工程所用之任何材料均應為新品，其品質、性能、成分、強度等規格應符合圖說規範。
3. 所謂同等品者包括是本產品，材料等產品，符合下列原則
(1)符合設計原意。(2)不影響原設計之空間及尺寸。(3)品質相當；規格，性能相符。(4)無損美觀。(5)可用性相當。(6)使用操作便利。(7)有其安全上之顧慮者，必須取得該管檢驗機構之安全證明書。

伍、施工與檢驗：

1、凡所選用之建材，須送樣經監造單位及業主認可後方得施工，承包廠商所選用之樣本，未能符合監造單位或業主要求時，得由監造單位或業主指定。
2、承包廠商須確實按照核定圖樣施工，如原計畫有未盡理想之處，欲變更原設計時，承包廠商須事先提出檢核，辦理變更手續，經核准後再行施工，切勿擅自變更。
3、材料進場、儲存、清點、檢測、查驗等依本工程規範辦理。
4、如經檢驗不合格者，承包廠商應即依指示作無償之改善，拆除重作或廢除，且在未改善前，不得擅自施工或使用，否則監造單位或業主得勒令停工，其一切後果責任概由承包廠商負責。
5、雖經監造單位及業主複測或檢驗之工程，承包廠商應負其全責，如需試驗者，其試驗費用(人工・材料)除另有規定外，檢驗合格，試驗費用由業主負擔，檢驗不合格，試驗費用由承包廠商負擔。
6、以上有關施工詳細圖繪製、材質證明檢測報告等，均含於本工程內，不另列單價計費。

陸・工程進度紀錄

1、承包廠商需依業主及監造單位核准之格式每日確實填寫施工日誌。
2、承包廠商應依照工程進度之需要攝取不同角度之工程進度照片資料，註明工程名稱、地點、日期、施工項目及位置，資料份數依工程合約規定送交業主存檔備查。

柒、補充說明：

1、承包廠商須依據本工程規範，得標後7天內提出本工程之標準施工流程及停檢點，並由監造單位審核後方可施工，其費用已含於工程費中，不另列單價計費。
2、本圖尺寸僅供參考，施工前承包廠商應現場丈量各部份尺寸，配合現場尺寸放樣，圖說若有不合理狀況，應即報監造單位，並依指示辦理。
3、本工程使用建材，如須工廠加工製造，製造之工廠，應有工廠登記證，符合CNS規定，產品檢附出廠登記證明，附依工程合約規定之保固書，並提出產品維護使用手冊。
4、承包廠商提出之標準施工流程須實際操作一次，經監造單位認定後依序執行。
5、以上有關施工詳細圖繪製，含於本工程內，不另列單價計費。
6、本工程拆除損壞設施，承包廠商均應以原飾材或相似飾材負修復之責，其工程費已含於拆除工程工項中，不另列單價計費
7、本工程水電設施銜接原有電力系統，並配合增設必要設施，費用均含於本工程內，不另列單價計費；承包廠商應依使用單位需求繪製配線施工詳圖，審核後方得施作。
8、本工程現有管線，不論執行拆除或新設工項時，均不得有損壞；如有損壞，由承包廠商負全責。
9、本工程材料有涉及顏色者，承包廠商須提送色卡及色樣，經監造單位及業主選定核可後，方可進場施作。
10、本工程新增所有外露轉角均須保持圓滑，完成後不得有說利之轉角及粗糙面產生。
11、承包廠商應有專業立場，對工程品質須有一定水準，如須檢驗不合格時，應修正至合格或拆除重作。

120

新竹縣竹北市公所(Zhubei City Office, Hsinchu County)

75

工程名稱 (Project Name)	清潔隊工作場所改善工程		
監造單位 (Construction Supervisor)	邑程建築師事務所	設計單位 (Designer)	邑程建築師事務所
施工廠商 (Contractor)		工程概要 (Project Descriptions)	
施工期間 (Duration)	民國○○年○○月○○日至○○年○○月○○日 (DD/MM/YYYY~DD/MM/YYYY)		
工地主任或工地負責人 (Site Manager)		電話 (TEL)	
專任工程人員 (Contractor's Professional Engineer)		電話 (TEL)	
通報專線 (Complaints & Suggestions)	全民督工專線 (Hot Line and Internet address) 0800-009-609 http://www.pcc.gov.tw 政風單位 (Government Ethics Department) 電子郵件 ethics@mail.tygh.gov.tw 電話：(03)3606821		電子版領區域
經費來源 (Budgetary Sources)	1. 中央 ＿＿＿＿(千元)(Unit: NT$1,000) 2. 地方 ＿＿＿＿(千元)(Unit: NT$1,000)		
重要公告事項 (Notes)	1. ＿＿年(Yr)＿＿月(M)＿＿日(D): 2. ＿＿年(Yr)＿＿月(M)＿＿日(D):		

施工告示牌:


(1). 單位: CM
(2). 告示牌
(a)漆綠色底，白色正楷字體，線條及框
(b)"配合單位"欄由工地視實際情況填寫
(c)工程竣工驗收後由承商自行拆除處理
(3). 告示牌材質採用金屬材質，牌面之固定方式須另行處理


曾瑞宏

張號	
圖名	工程名稱
施工圖/施工說明	新竹縣竹北市公所清潔隊工作場所改善工程
繪圖	
設計	
修正	
校對	
日期	2025-06-30

台中沙鹿區台灣大道六段1059號
尚強技術顧問有限公司

比例尺	
圖號	A1-02

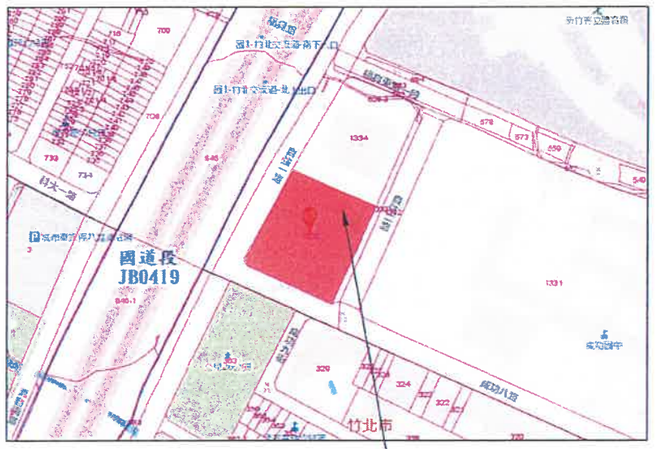
國道一
國道一
國道一

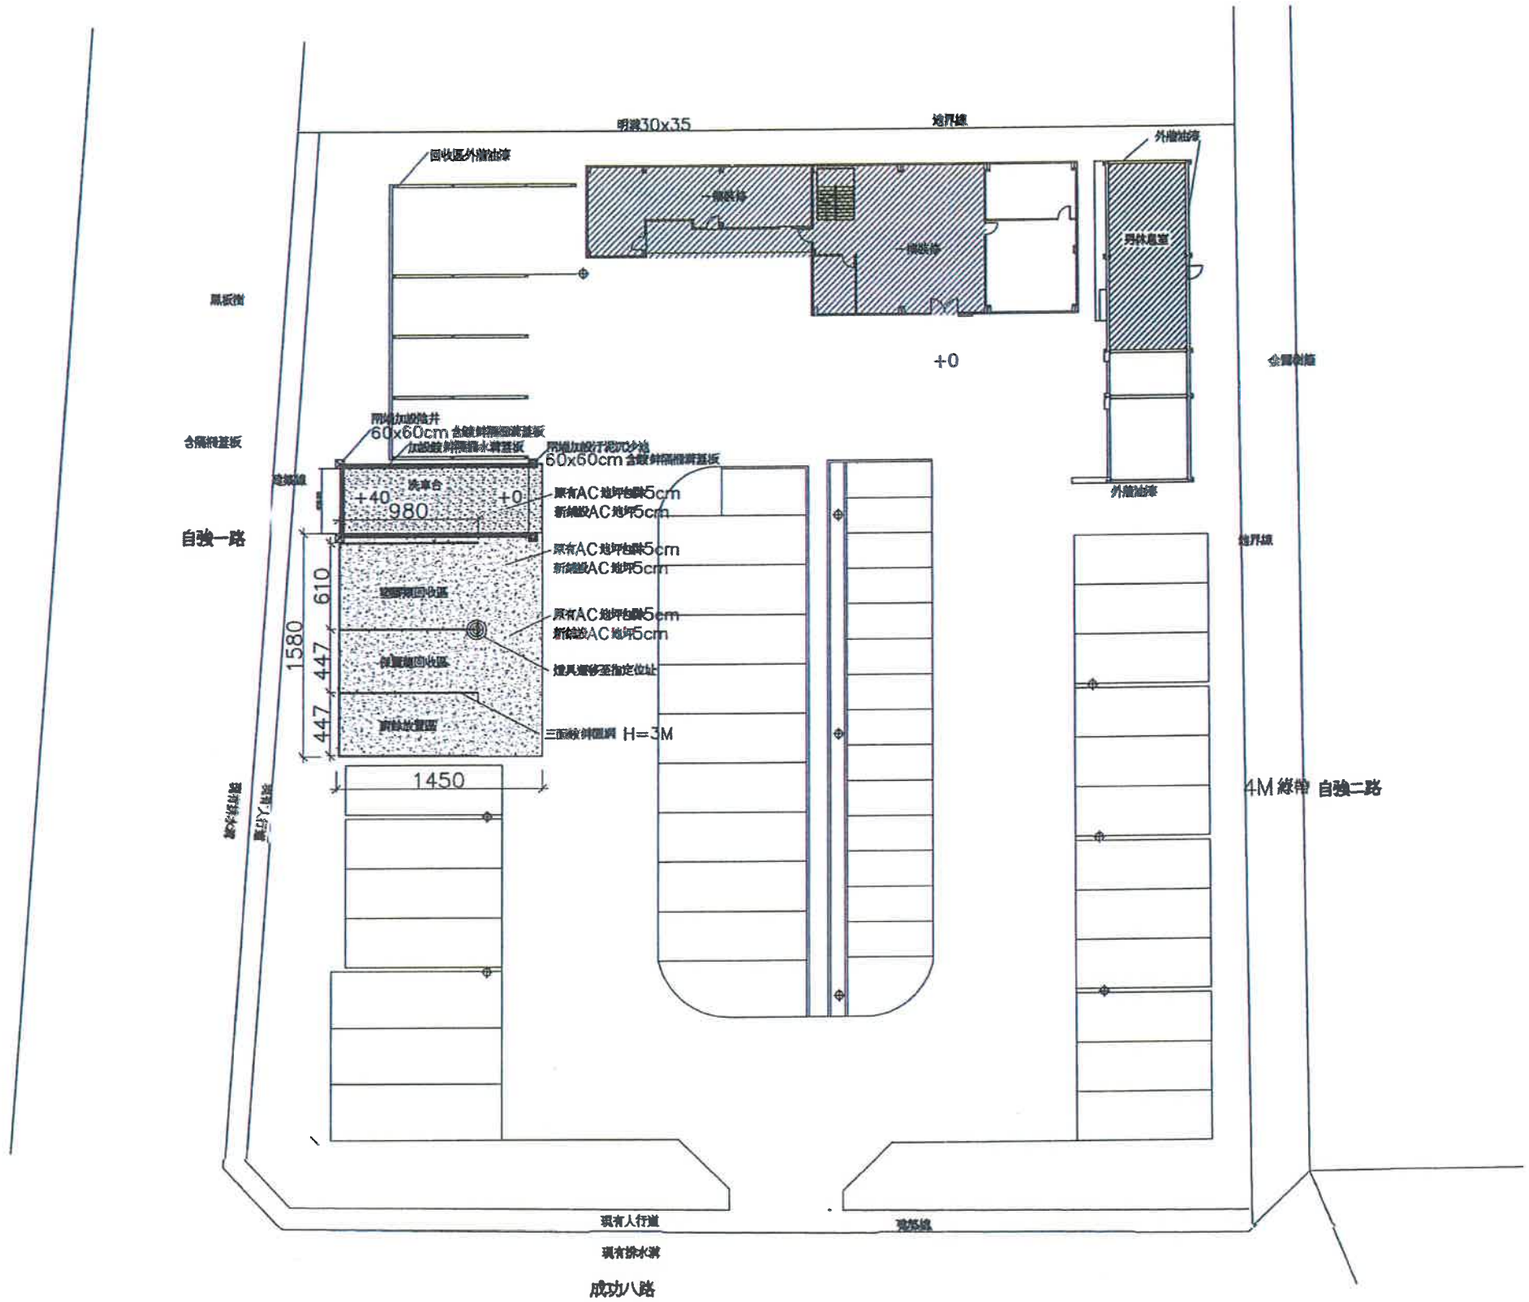


配置圖　S:1/400

張號	
圖名	工程名稱
基地配置圖	新竹縣竹北市公所清潔隊工作場所改善工程
繪圖	
設計	
修正	
校對	
日期	2025-06-30

尚強技術顧問有限公司
台中沙鹿區台灣大道六段1059號

比例尺	
圖號	A2-02

曾瑞宏

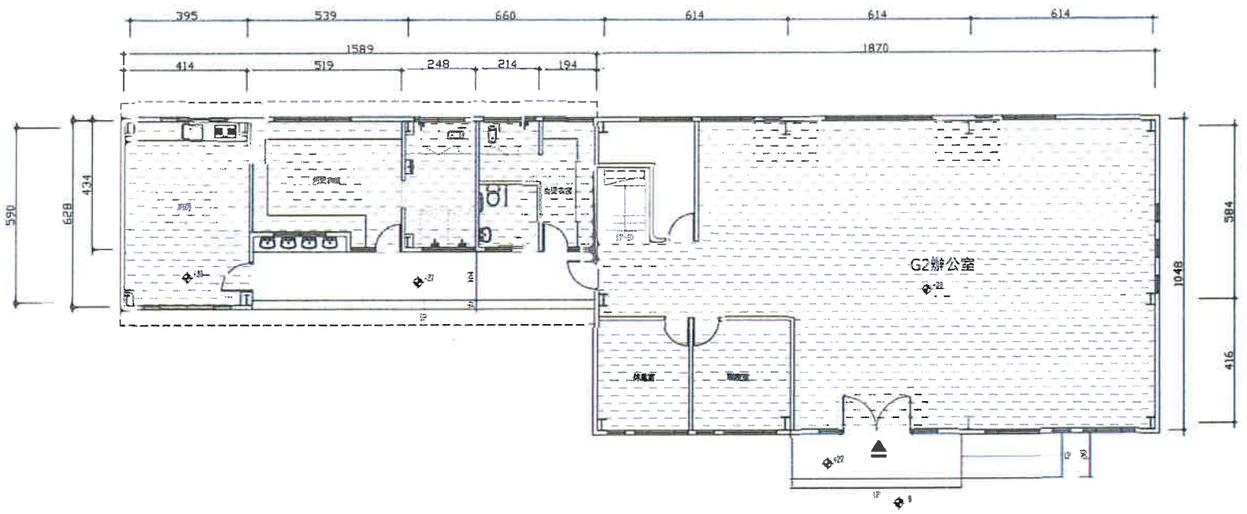


原使照核准壹層平面圖

SCALE:1/100



G2辦公室	項目	室內面積計算式
	壹層樓地板面積	18.7*10.48+15.89*6.28=295.77㎡

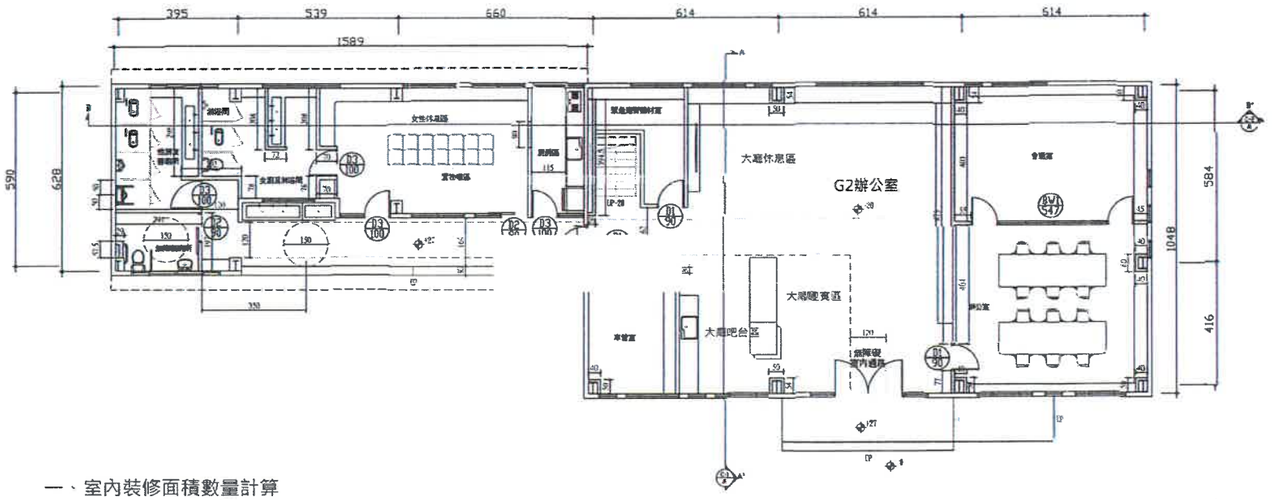

地上壹層裝修平面圖

SCALE:1/100

一、室內裝修面積數量計算

新增分間牆9mm矽酸鈣板 (耐燃1級/綠建材)：

0.9*2+(0.26+3.945+0.45+0.6+0.4+0.4+0.5+0.93+0.4+0.41+1.55+0.2+1.43+0.5+0.54+0.5+0.54+8.73+0.77+0.4+0.54+4.03)+(0.55*2)+4.04+0.4+0.54+0.5+0.4+(0.45*2)+0.4+0.6+0.4+0.4+0.5)*3.3+(3.3-2.1)*0.9*2*2 =136.34㎡

面刷水泥漆(綠建材):136.34㎡

新增分間牆 1/2b磚牆

2.98+2.02+0.78+2.08+0.72+2.08+0.7+0.7+0.78+2.87+1.97+0.25+0.575*2.9=53.66㎡

面刷水泥漆(綠建材):53.66㎡

二、法規檢討

避難層出入口數量及寬度檢討

本案原使用用途G-2辦公室樓地板面積295.77m²<500m²，

本案出入口寬度 1.2m > 1.2m ...ok

本案出入口高度 2.3m > 1.8m ...ok

依原核准符合建築設計施工編第九十之一條規定，

走廊淨寬度檢討

本案G-2辦公室樓地板面積295.77m²>200m²，

本案走廊淨寬度 1.2m = 1.2m ...ok

符合建築設計施工編第九十二條規定。

防火區劃檢討

本案防火區劃未變更，G-2辦公室樓地板面積295.77m²<1500m² ...ok

依原核准防火區劃，符合建築設計施工編第七十九條、第七十九條之二、第二百零三條、第二百四十二條規定。

分間牆檢討-以不燃材料建造符合規定。

內部裝修材料檢討

本案新增分間牆9mm矽酸鈣板(耐燃1級) ...ok

符合建築設計施工編第八十八條規定。

防火構造之限制檢討

本案用途G-2辦公室位於一層，樓地板面積295.77m²，

依原核准構造現況，符合建築設計施工編第六十九條G類規定。

停車空間檢討

本案G-2辦公室總樓地板面積485.51m²，依原核准竣工設置 ...ok

無障礙設施檢討

本案變更無障礙廁所範圍依規定設置，


符合建築技術規則建築設計施工編第十章無障礙建築物之規定 ...ok

曾瑞宏


張號	
圖名	原始照核准地上一層平面圖
工程名稱	新竹縣竹北市公所清潔隊工作場所改善工程
繪圖	
設計	
修正	
校對	
日期	2025-06-30


尚強技術顧問有限公司
台中沙鹿區台灣大道六段1059號

比例尺	
圖號	A2-03

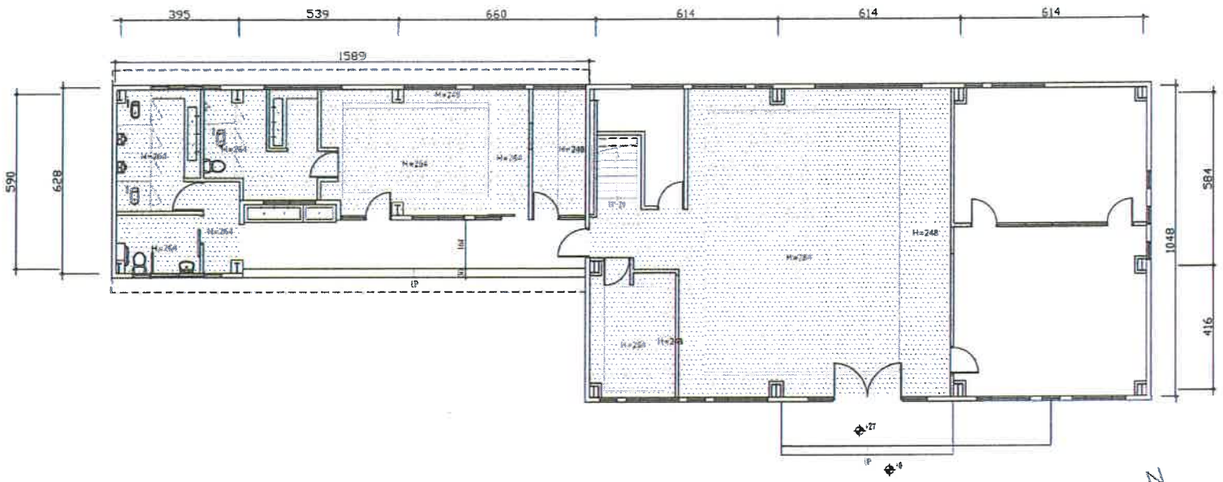

地上壹層天花板平面圖
SCALE:1/100

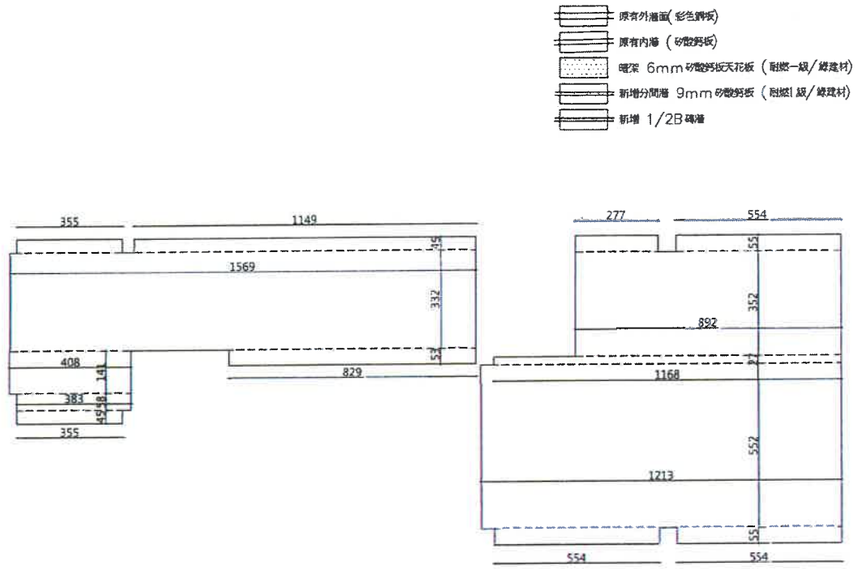

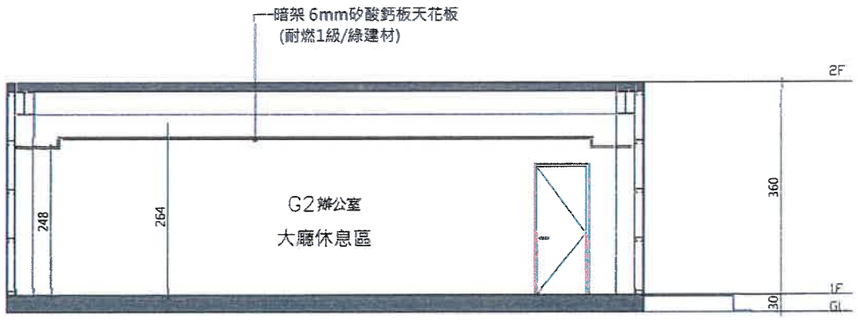


C-1 / A G2辦公室A-A'剖立面圖
SCALE:1/50

天花板裝修面積數量計算:

新增暗架 6mm矽酸鈣板天花板 (耐燃一級/綠建材)

(3.55+11.49)*0.45+15.69*3.32+8.29*0.53+4.08*1.41+3.83*0.58+3.55*0.45+(2.77+5.54)*0.55
+8.92*3.52+11.68*0.27+12.13*5.52+(5.54+5.54)*0.55=184.73m²

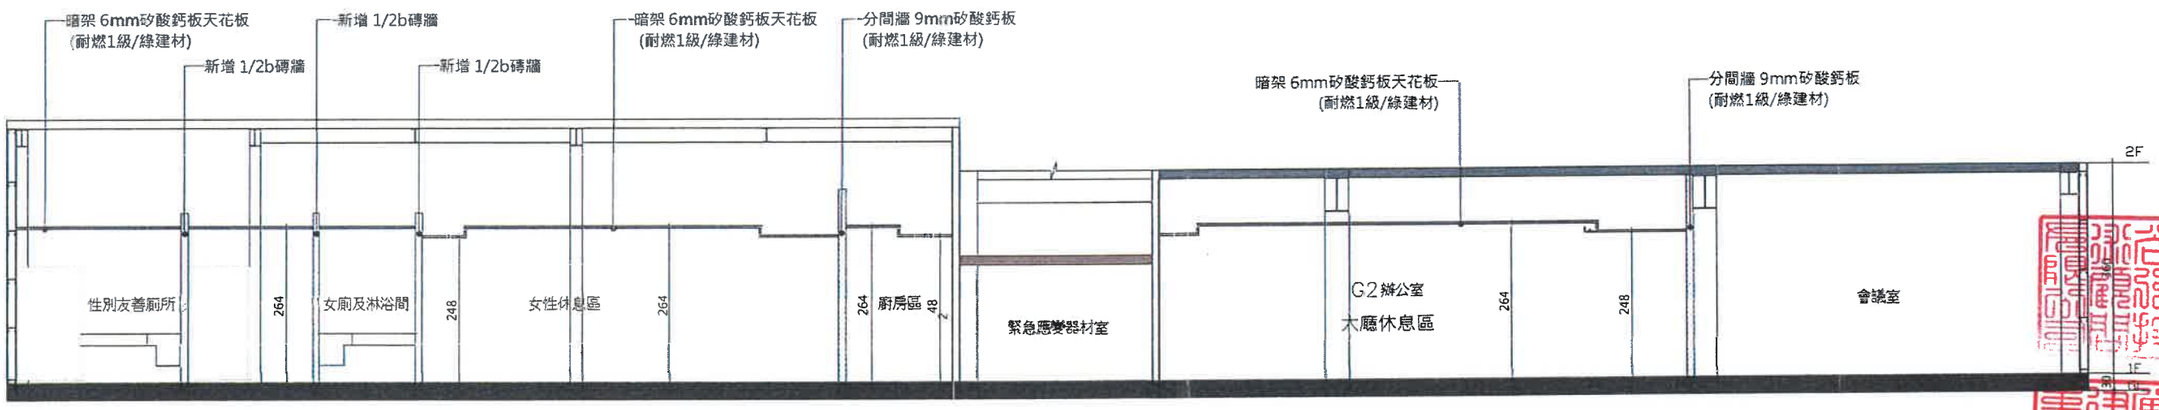

C-2 / A G2辦公室B-B'剖立面圖
SCALE:1/50

曾瑞宏



張號	
圖名	工程名稱
地上一層平面圖/天花板/剖立面圖	新竹縣竹北市公所清潔隊工作場所改善工程
總圖	
設計	
修正	
校對	
日期	2025-06-30


尚強技術顧問有限公司
台中沙鹿區台灣大道六段1059號

比例尺


圖號 A2-04

門窗圖

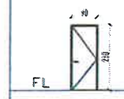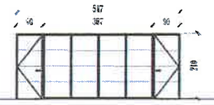編號	D1	D2	D3	BW1
門窗立面形式				
尺寸	木質門90*210	橫拉木質門90*210	三合一鋁門100*210	烤漆鋁框炭玻璃門，5mm強化清玻璃 547*210

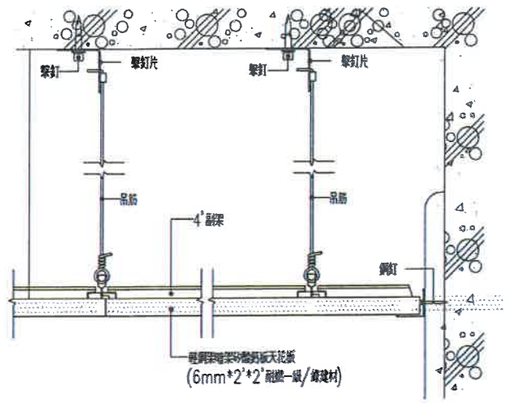

輕鋼架天花板剖面示意圖
(耐燃一級/綠建材)

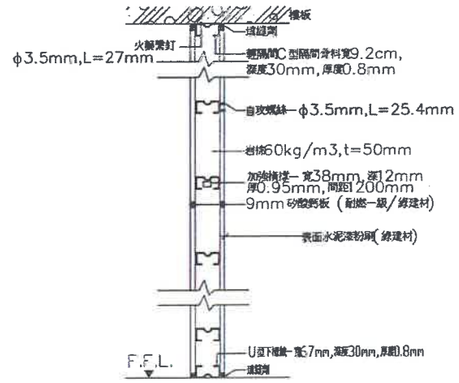

矽酸鈣板分間牆細部剖面大樣圖
SCALE:1/10(耐燃一級/綠建材)

第十章 無障礙建築物專章檢討

第170條 無障礙建築物應用範圍如下表：

建築物無障礙設施 / 建築物之應用範圍	通路			樓梯			升降設備			廁所 盥洗室				停車空間		
	室外	室內出入口	避難層坡道扶手	扶手	樓梯設計	扶手（欄杆）	警鈴設施	引導設施	出入口	機廂門	機廂	廁所	馬桶及扶手	小便器	洗面盆	浴室	引導設施	停車空間	殘障停車位
建築技術規則建築設計施工編§7條		v	v									v	v	v	v				
G—2辦公室 已設計成無障礙設施		v	v									v	v	v	v				

v：表建築物應設置該無障礙設施

建築技術規則 第十章 無障礙建築物

條文	設計內容	檢討結果
第一百六十七條之一		OK
第一百六十七條之二		OK
第一百六十七條之三		OK
第一百六十七條之四		OK
第一百六十七條之五		OK

樓地板面積區段	樓梯寬度區段
五十坪以下	一
五十一坪—一百坪以下	二
一百坪以下—一百二十五坪以下	三
一百二十五坪以下—一百五十坪以下	四
一百五十坪以下—一百七十五坪以下	五
一百七十五坪以下—二百坪以下	六
二百坪以下—二百二十五坪以下	七
二百二十五坪以下—二百五十坪以下	八
二百五十坪以下—三百坪以下	九
三百坪以下—三百五十坪以下	十
三百五十坪以下—四百坪以下	十一
四百坪以下—四百五十坪以下	十二
四百五十坪以下—五百坪以下	十三

第一百六十七條之六		OK
第一百六十七條之七		OK

建築物無障礙設施設計規範　　內政部 108年 07月 01日


規範	設計內容	檢討結果
203 室外通路		
		OK
		OK
		OK
		OK
		OK
		OK
		OK
		OK
		OK

規範	設計內容	檢討結果
204 室內通路走廊		
		OK
		OK
		OK
		OK
		OK


規範	設計內容	檢討結果
205 出入口		
		□OK
		□OK

規範	設計內容	檢討結果
205 出入口(續)		
		□OK
		□OK
		□OK
		□OK

規範	設計內容	檢討結果
第五章 廁所盥洗室		OK

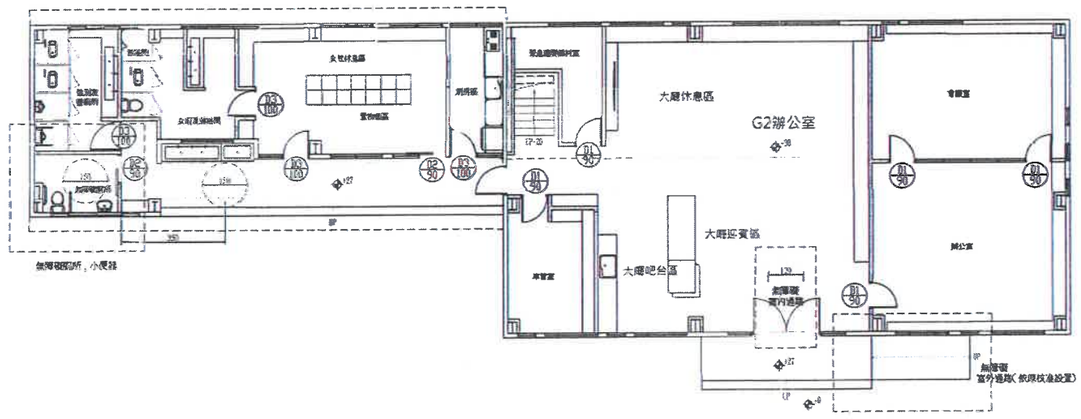

裝修後地上壹層平面圖
SCALE:1/100

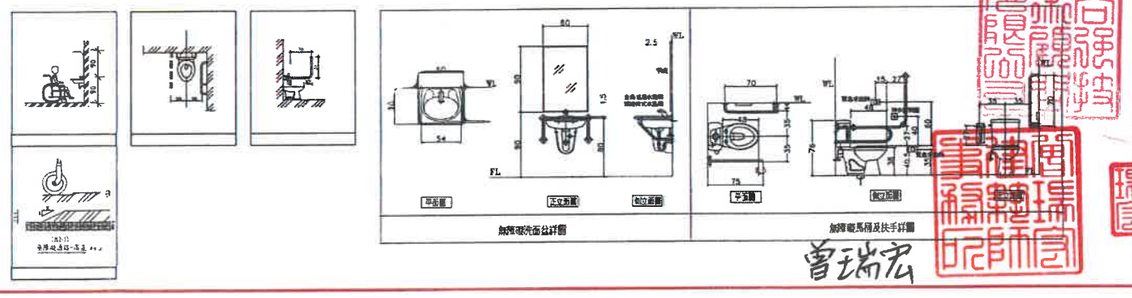

張號	
圖名	工程名稱
門窗圖／大樣圖／無障礙建築專章檢討	新竹縣竹北市公所清潔隊工作場所改善工程
總圖	
設計	
修正	
校對	
日期	2025-06-30
尚強技術顧問有限公司	台中沙鹿區台灣大道六段1059號
比例尺	
圖號	A2-05

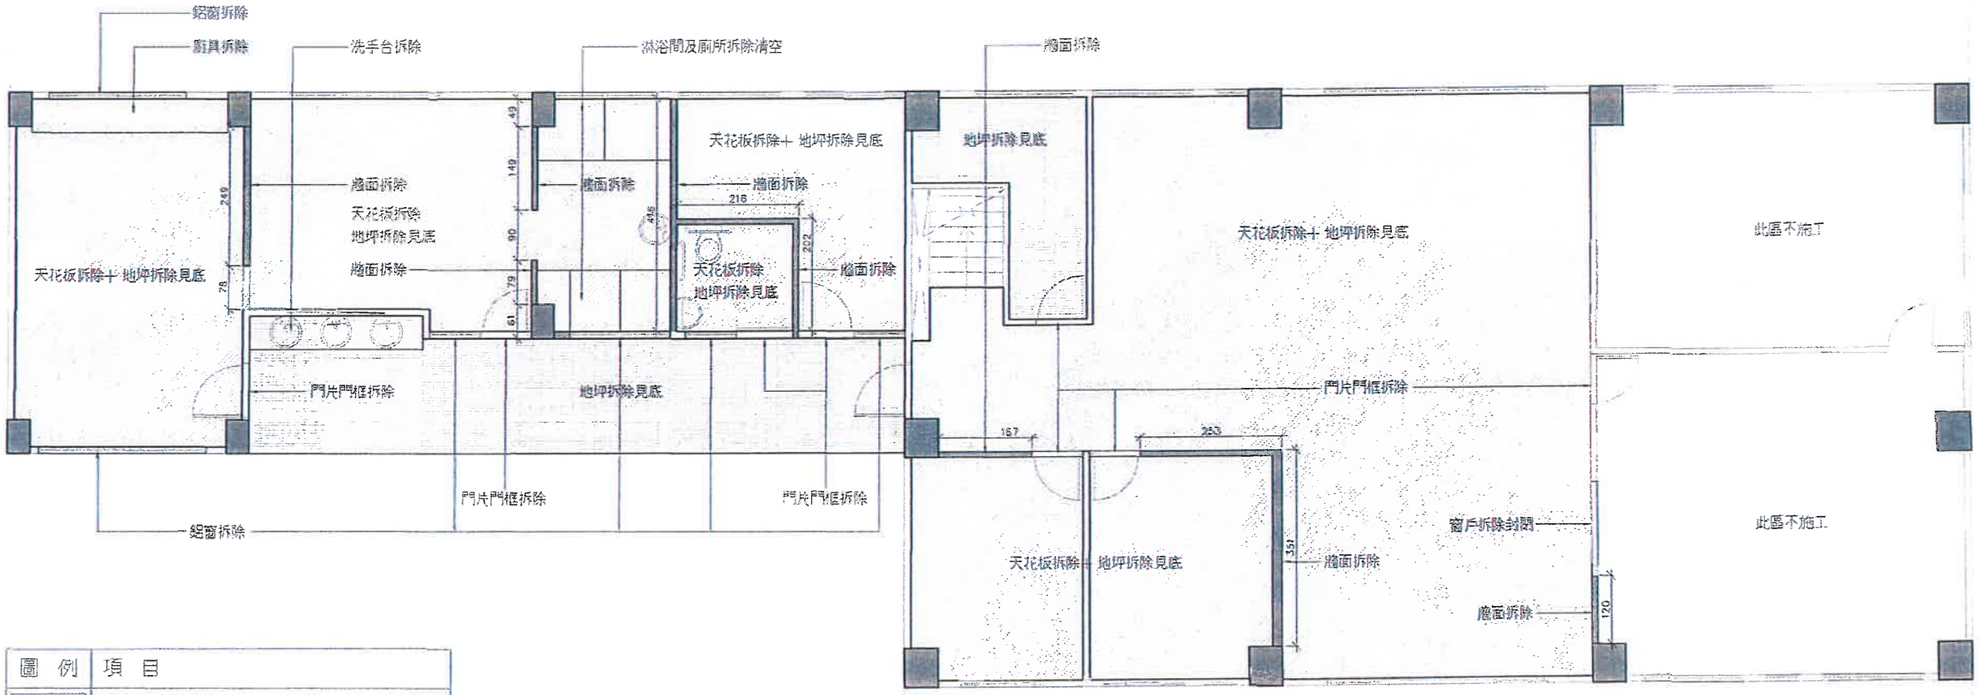


圖 例	項 目
	天花板拆除+ 地坪拆除見底
	地坪拆除見底
	牆面拆除
	鋁窗拆除
	門片門框拆除


一樓兩處拆除

1. 書櫃，檔案，桌椅，等，協助遷移至業主指定地點
2. OA 屏風拆除後協助遷移至業主指定地點
3. 窗簾拆除
4. 天花板風扇，空調出風口拆除清潔，新天花板[illegible]
5. 緊急照明燈，滅火器等設備遷移，室內粉刷完[illegible]

大廳及女性休息區拆除平面圖　S=1/100

曹瑞宏

張　號	
圖　名	大廳及女性休息區拆除平面圖
工程名稱	新竹縣竹北市公所清潔隊工作場所改善工程
繪　圖	
設　計	
修　正	
校　對	
日　期	2025-06-30
尚強技術顧問有限公司	台中沙鹿區台灣大道六段1059號
比例尺	
圖　號	A2-06

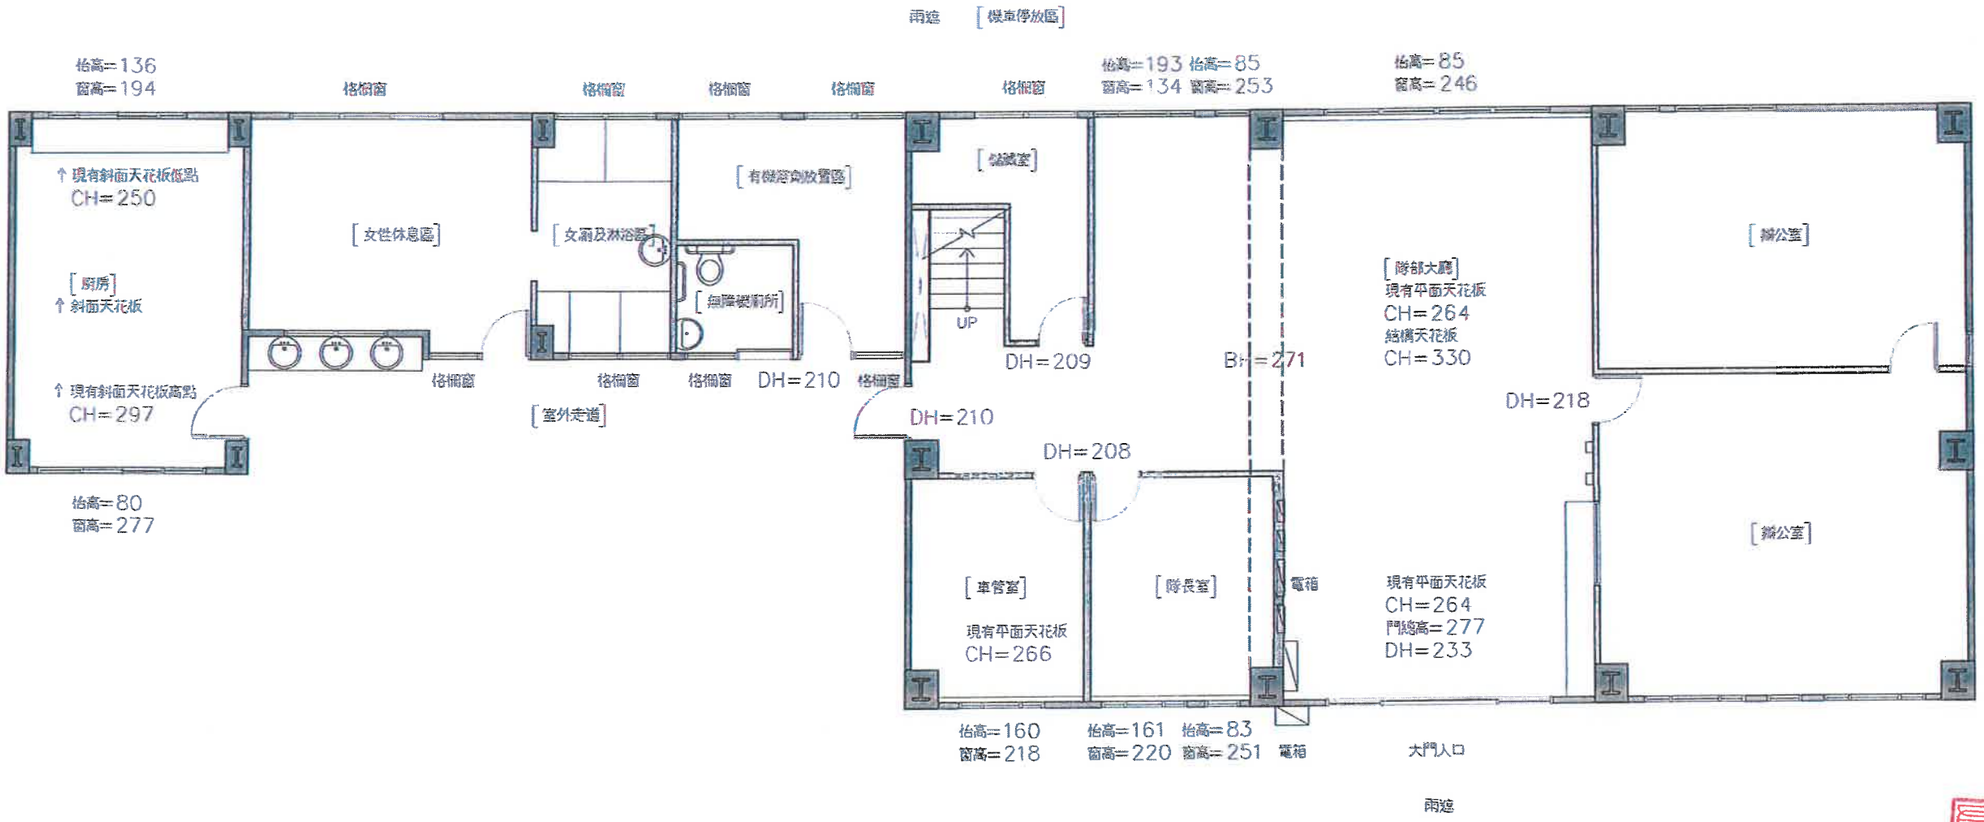


大廳及女性休息區原況平面圖　S=1/100

曾瑞宏

張　號	
圖　名	工程名稱
大廳及女性休息區原況圖	新竹縣竹北市公所清潔隊工作場所改善工程
繪　圖	
設　計	
修　正	
校　對	
日　期	2025-06-30

尚強技術顧問有限公司
台中沙鹿區台灣大道六段1069號

比例尺	
圖　號	A2-07

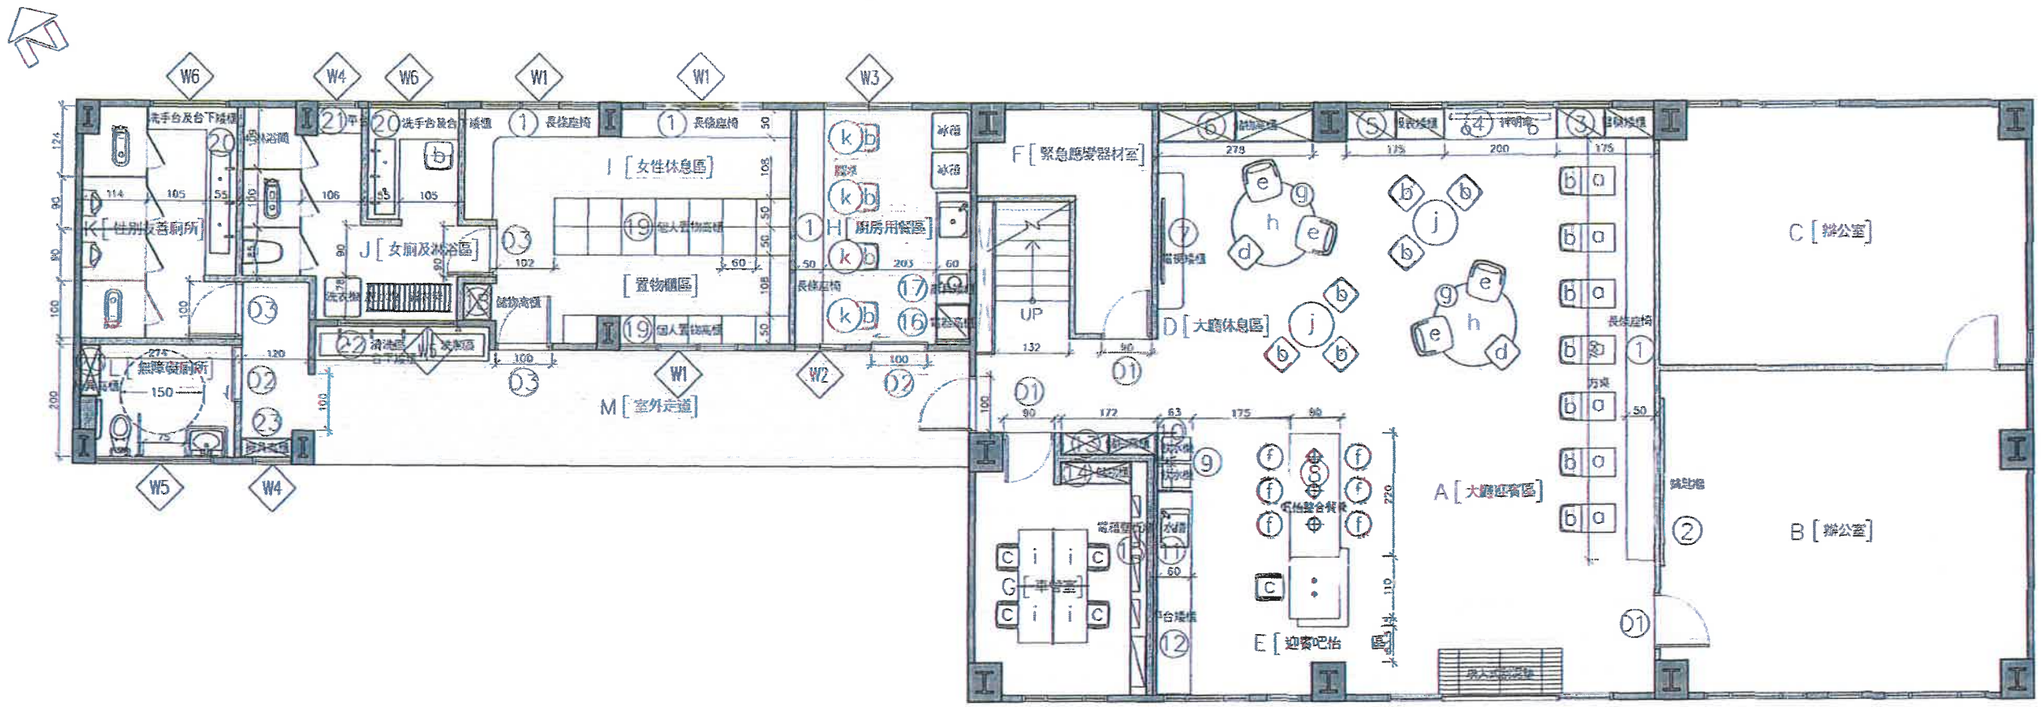

一般傢俱表	
圖例	項目
	a－長條椅方桌－L60xW50xH75cm
	b－椅背餐椅－L50xW50xH90cm (尺寸僅供參考)
	c－辦公椅－L50xW50xH90cm (尺寸僅供參考)
	d－無背座椅－L50xW50xH50cm (尺寸僅供參考)
	e－單人沙發－L70xW65xH90cm (尺寸僅供參考)
	f－矮吧檯椅－D50xH60cm (尺寸僅供參考)
	g－小邊桌－D40xH55cm
	h－圓形地毯－D=150cm
	i－一般辦公桌－L100xW60xH75cm
	j－圓形餐桌－D80xH75cm
	k－長條椅圓桌－D60xH75cm

分區表
A－大廳迎賓區
B－辦公室－1
C－辦公室－2
D－大廳休息區
E－吧檯餐桌區
F－緊急應變器材室
G－車管室
H－廚房用餐區
I－女性休息區
J－女廁及淋浴區
K－性別友善廁所
L－無障礙廁所
M－室外走道區

木作傢俱索引表			
圖號	項目	圖號	項目
A3－2	①長條座椅	A3－4	⑭車管室儲物高櫃
A3－3	②鑰匙櫃木作壁板	A3－10	⑮車管室電箱壁板箱
A3－1	③醫藥矮櫃	A3－5	⑯廚房電器高櫃
A3－1	④神明桌組	A3－5	⑰廚房廚具矮櫃
A3－1	⑤報表矮櫃	A3－5	⑱儲物高櫃
A3－1	⑥儲物高櫃	A3－6	⑲個人置物高櫃
A3－2	⑦電視矮櫃	A3－7	⑳洗手台及抬下矮櫃
A3－2	⑧迎賓吧檯整合餐桌	A3－7	㉑平台
A3－3	⑨飲水機矮櫃	A3－8	㉒洗手台及抬下矮櫃
A3－3	⑩置物層板X2	A3－8	㉓掃具高櫃
A3－3	⑪主題牆壁板及文字		
A3－3	⑫平台矮櫃		
A3－4	⑬走廊儲物高櫃		

大廳及女性休息區平面配置圖　S=1/100

曾瑞宏

張號

圖名：大廳及女性休息區平面配置圖

工程名稱：新竹縣竹北市公所清潔隊工作場所改善工程

繪圖

設計

修正


校對

日期：2025-06-30

尚強技術顧問有限公司
台中沙鹿區台灣大道六段1059號

比例尺


圖號：A2-08

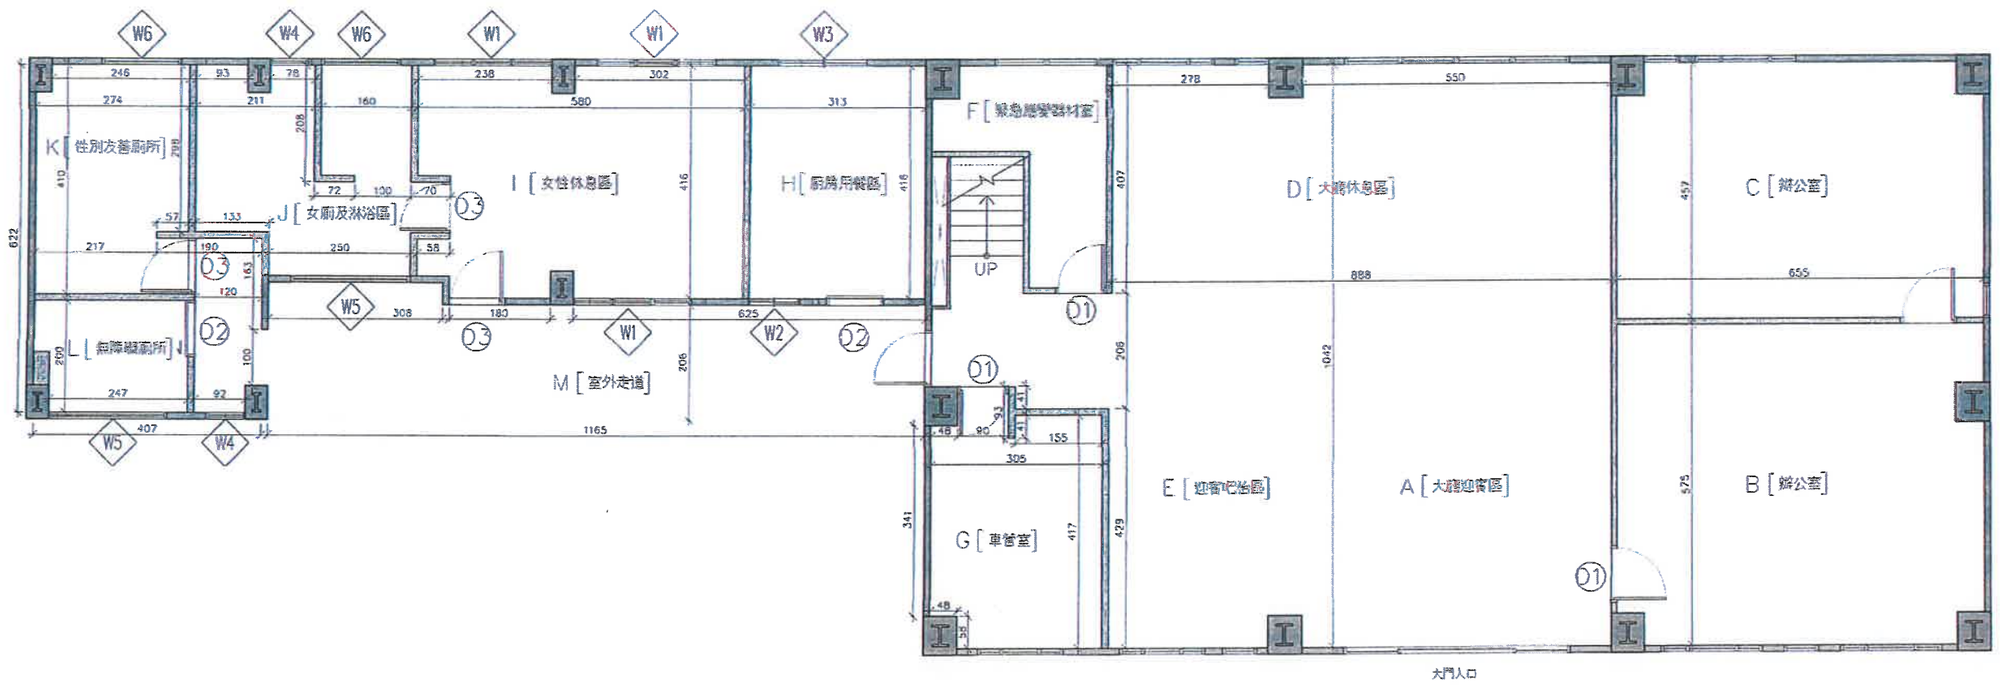

大廳及女性休息區平面尺寸圖　S=1/100

曾瑞宏


張　號	
圖　名	大廳及女性休息區平面尺寸圖
工程名稱	新竹縣竹北市公所清潔隊工作場所改善工程
繪　圖	
設　計	
修　正	
校　對	
日　期	2025-06-30
尚強技術顧問有限公司	台中沙鹿區台灣大道六段1059號
比例尺	
圖　號	A2-09

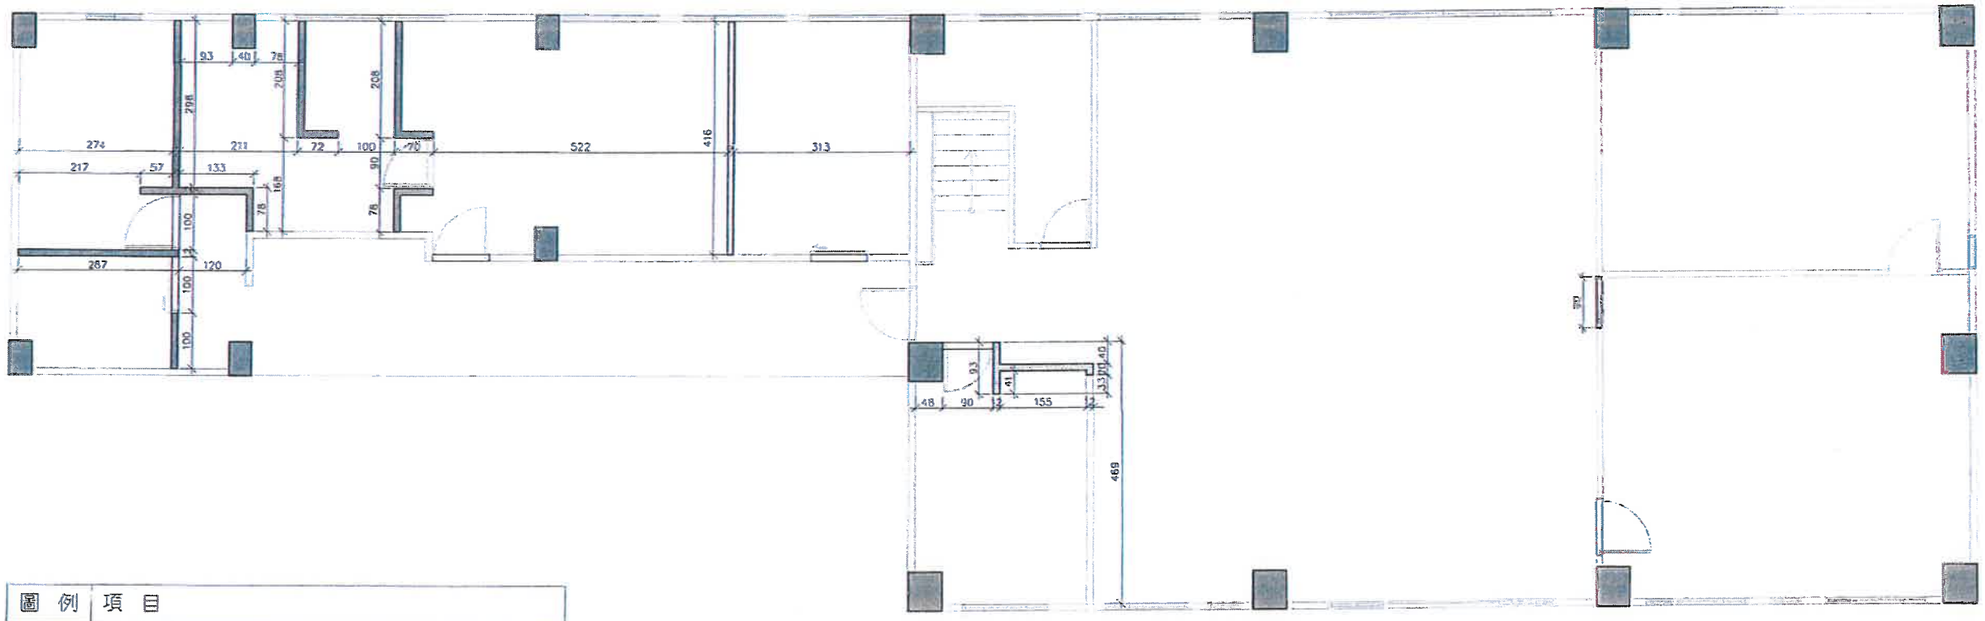

圖例	項目
	砌 1/2B 磚隔間工程 H=290cm
	9mm 雙面單層矽酸鈣板隔間 H=330cm
	新做門組

大廳及女性休息區隔間牆配置圖　S=1/100

張號	
圖名	大廳及女性休息區隔間牆配置圖
工程名稱	新竹縣竹北市公所清潔隊工作場所改善工程
繪圖	
設計	
修正	
校對	
日期	2025-06-30
	尚強技術顧問有限公司 台中沙鹿區台灣大道六段1059號
比例尺	
圖號	A2-10

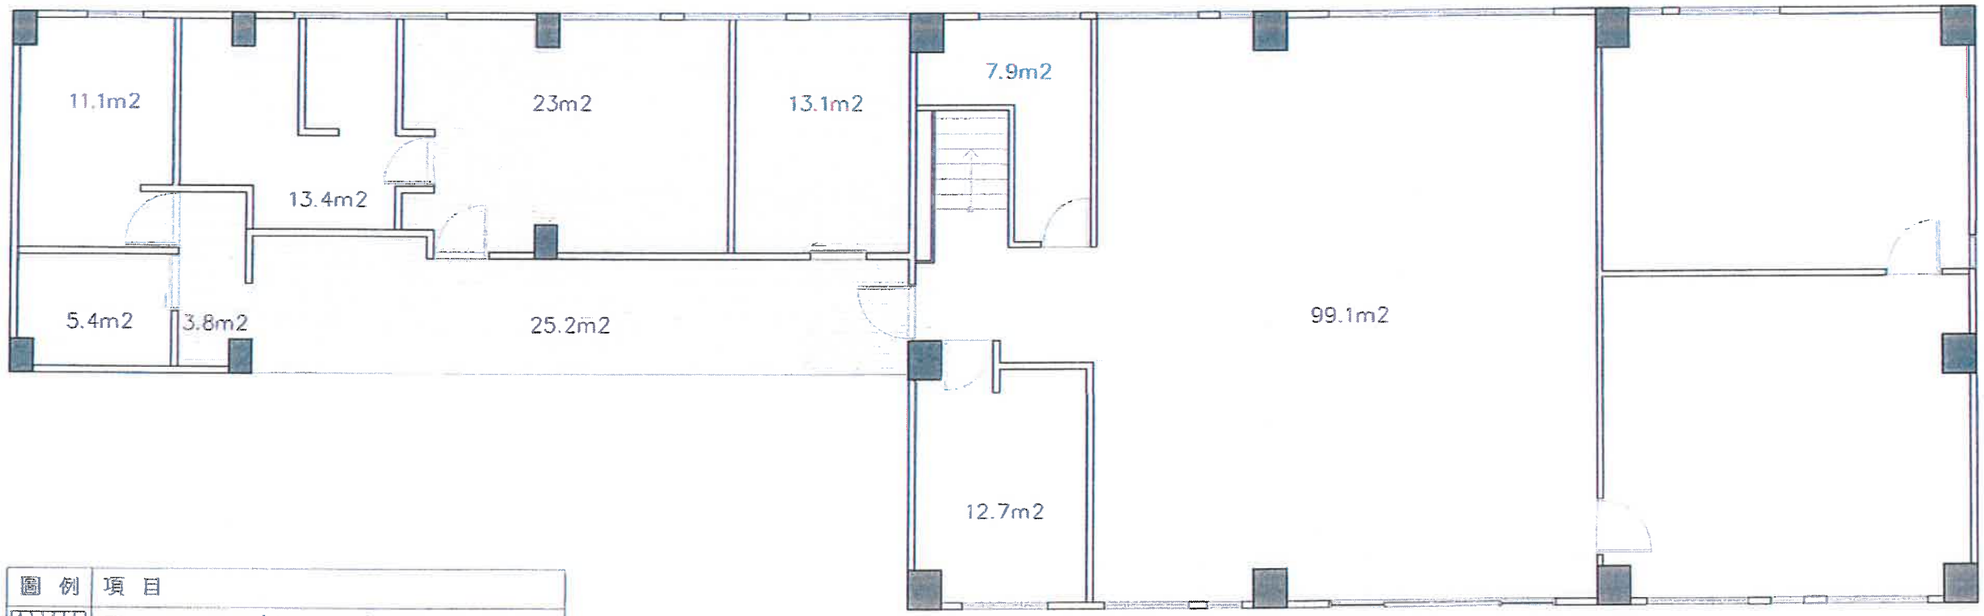

圖例	項目
	霧面止滑石英磚（60X60）
	霧面止滑磁磚（30X30）
	木紋磚
	新做門組


大廳及女性休息區地坪配置圖　S=1/100

曾瑞光

張號	
圖名	工程名稱
大廳及女性休息區地坪配置圖	新竹縣竹北市公所清潔隊工作場所改善工程
繪圖	
設計	
修正	
校對	
日期	2025-06-30

尚強技術顧問有限公司
台中沙鹿區台灣大道六段1059號

比例尺	
圖號	A2-11

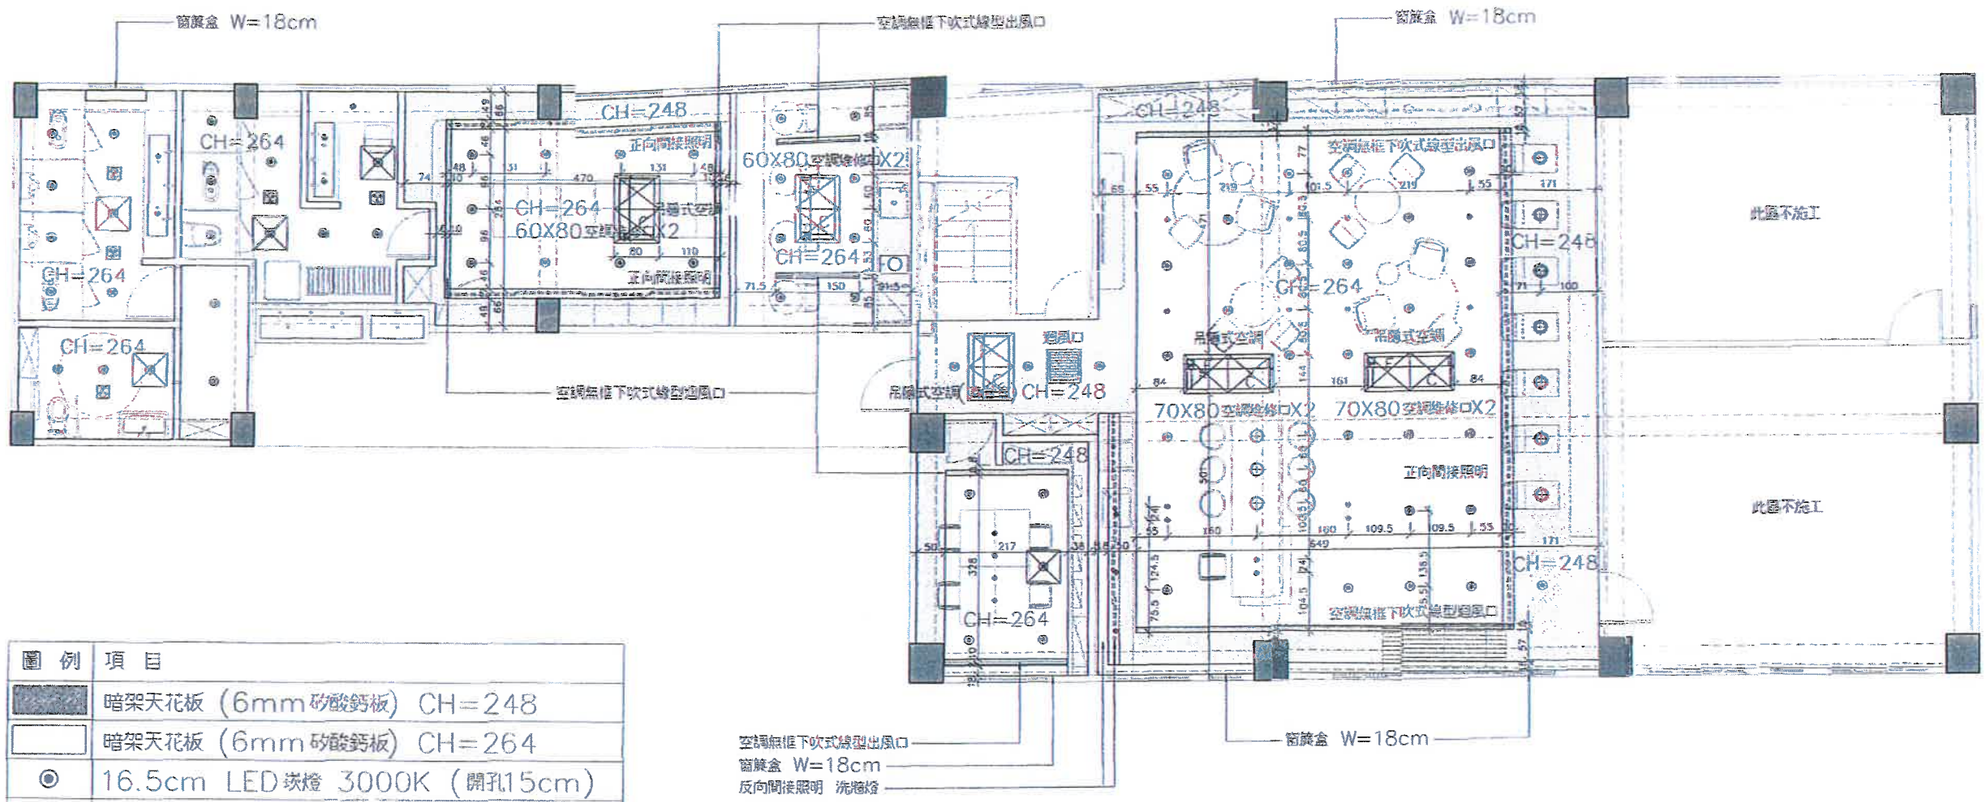

圖例	項目
	暗架天花板 (6mm矽酸鈣板) CH=248
	暗架天花板 (6mm矽酸鈣板) CH=264
◉	16.5cm LED崁燈 3000K (開孔15cm)
⊙	8.5cm LED崁燈 3000K (開孔7.5cm)
⊕	吧檯區吊燈 3000K
⊕	座位區吊燈 3000K
	LED T5 串接燈管 4000K
	浴廁抽風扇 (23X23cm)
	空調維修口 (60X80cm)
	一般維修口 (60X60cm)

大廳及女性休息區天花板圖 S=1/100

曾瑞宏

張號	
圖名	工程名稱
大廳及女性休息區天花板圖	新竹縣竹北市公所清潔隊工作場所改善工程
繪圖	
設計	
修正	
校對	
日期	2025-06-30
尚強技術顧問有限公司 台中沙鹿區台灣大道六段1059號	
比例尺	
圖號	A2-12

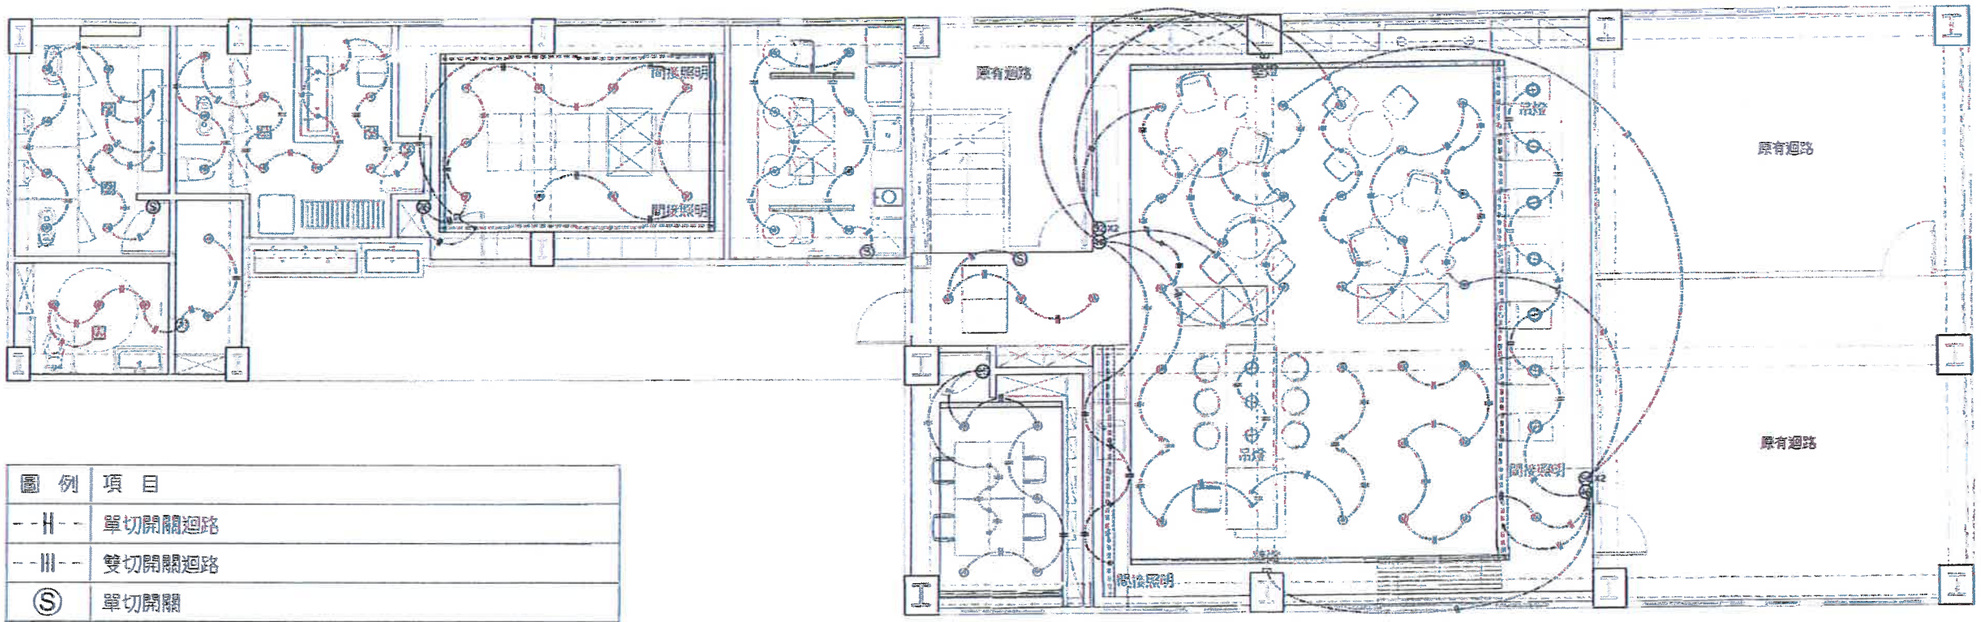


圖 例	項 目
--H--	單切開關迴路
--III--	雙切開關迴路
Ⓢ	單切開關
ⓢ2	二聯單切開關
ⓢ3	三聯單切開關
ⓢ2	雙切(雙控)開關
◉	16.5cm LED崁燈 3000K (開孔15cm)
◉	8.5cm LED崁燈 3000K (開孔7.5cm)
⊕	吧檯區吊燈 3000K
⊕	座位區吊燈 3000K
----------	LED T5 串接燈管 4000K
▣	浴廁抽風扇 (23X23cm)
▭	LED壁燈

大廳及女性休息區燈具迴路圖 S=1/100

曾瑞宏

張 號	
圖 名	工程名稱
大廳及女性休息區燈具迴路圖	新竹縣竹北市公所清潔隊工作場所改善工程
繪 圖	
設 計	
修 正	
校 對	
日 期	2025-06-30

尚強技術顧問有限公司
台中沙鹿區台灣大道六段1059號

比例尺	
圖 號	A2-13


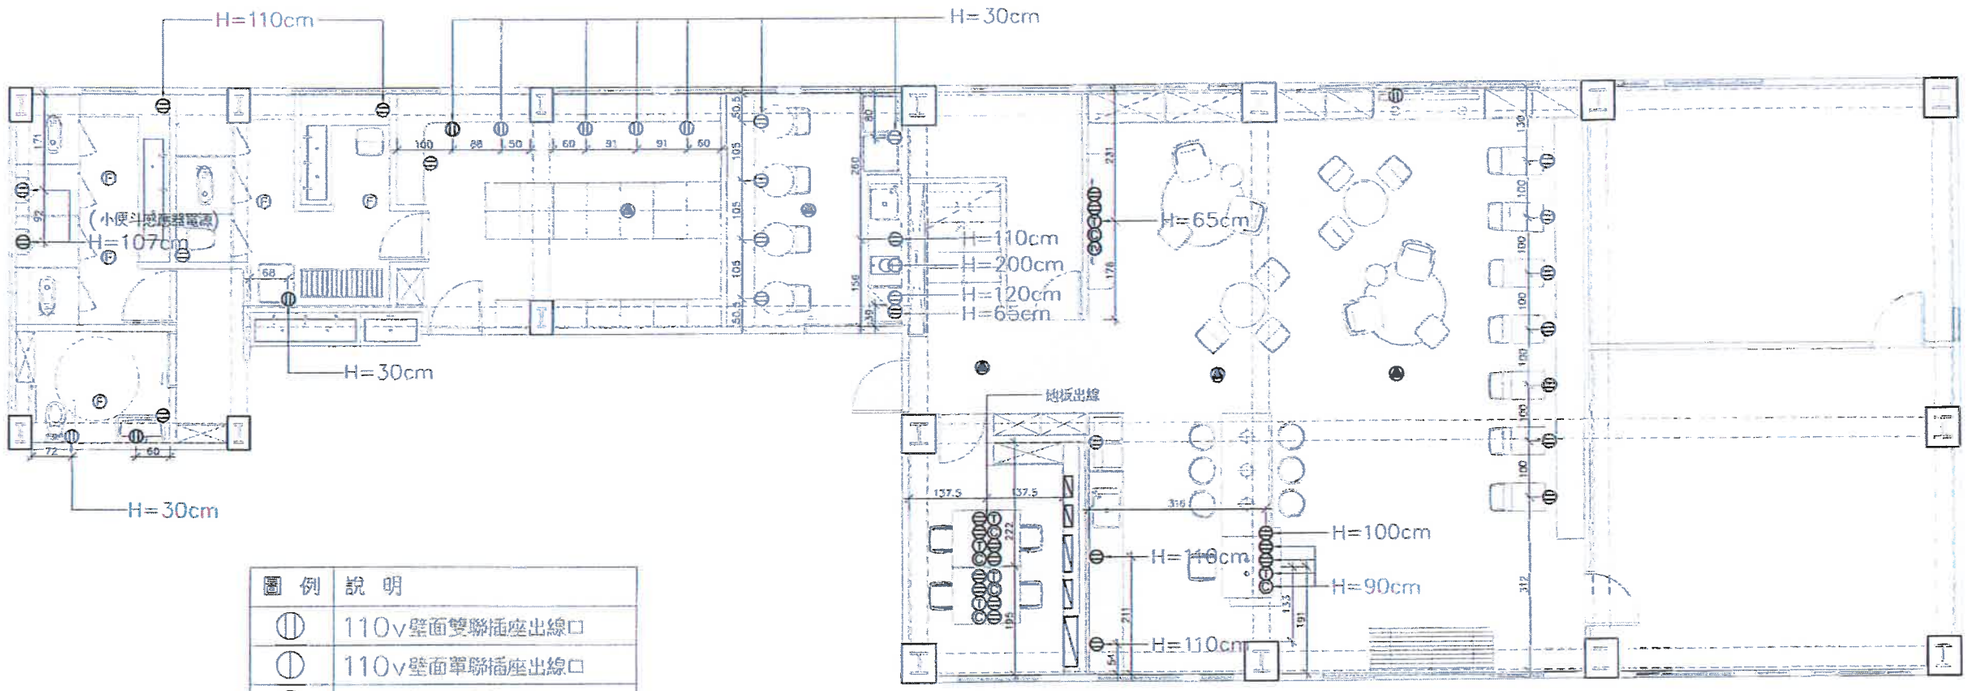


圖 例	說 明
ⓓ	110v壁面雙聯插座出線口
ⓘ	110v壁面單聯插座出線口
Ⓕ	天花板內風機電源出線
Ⓣ	電話出線口
Ⓒ	網路出線口
Ⓣⓥ	電視出線口
	配電盤
	220v空調電源

大廳及女性休息區插座配置圖　S=1/100

曾瑞宏

張號	
圖名	工程名稱
大廳及女性休息區插座配置圖	新竹縣竹北市公所清潔隊工作場所改善工程
繪圖	
設計	
修正	
校對	
日期	2025-06-30
尚強技術顧問有限公司 台中沙鹿區台灣大道六段1069號	
比例尺	
圖號	A2-14

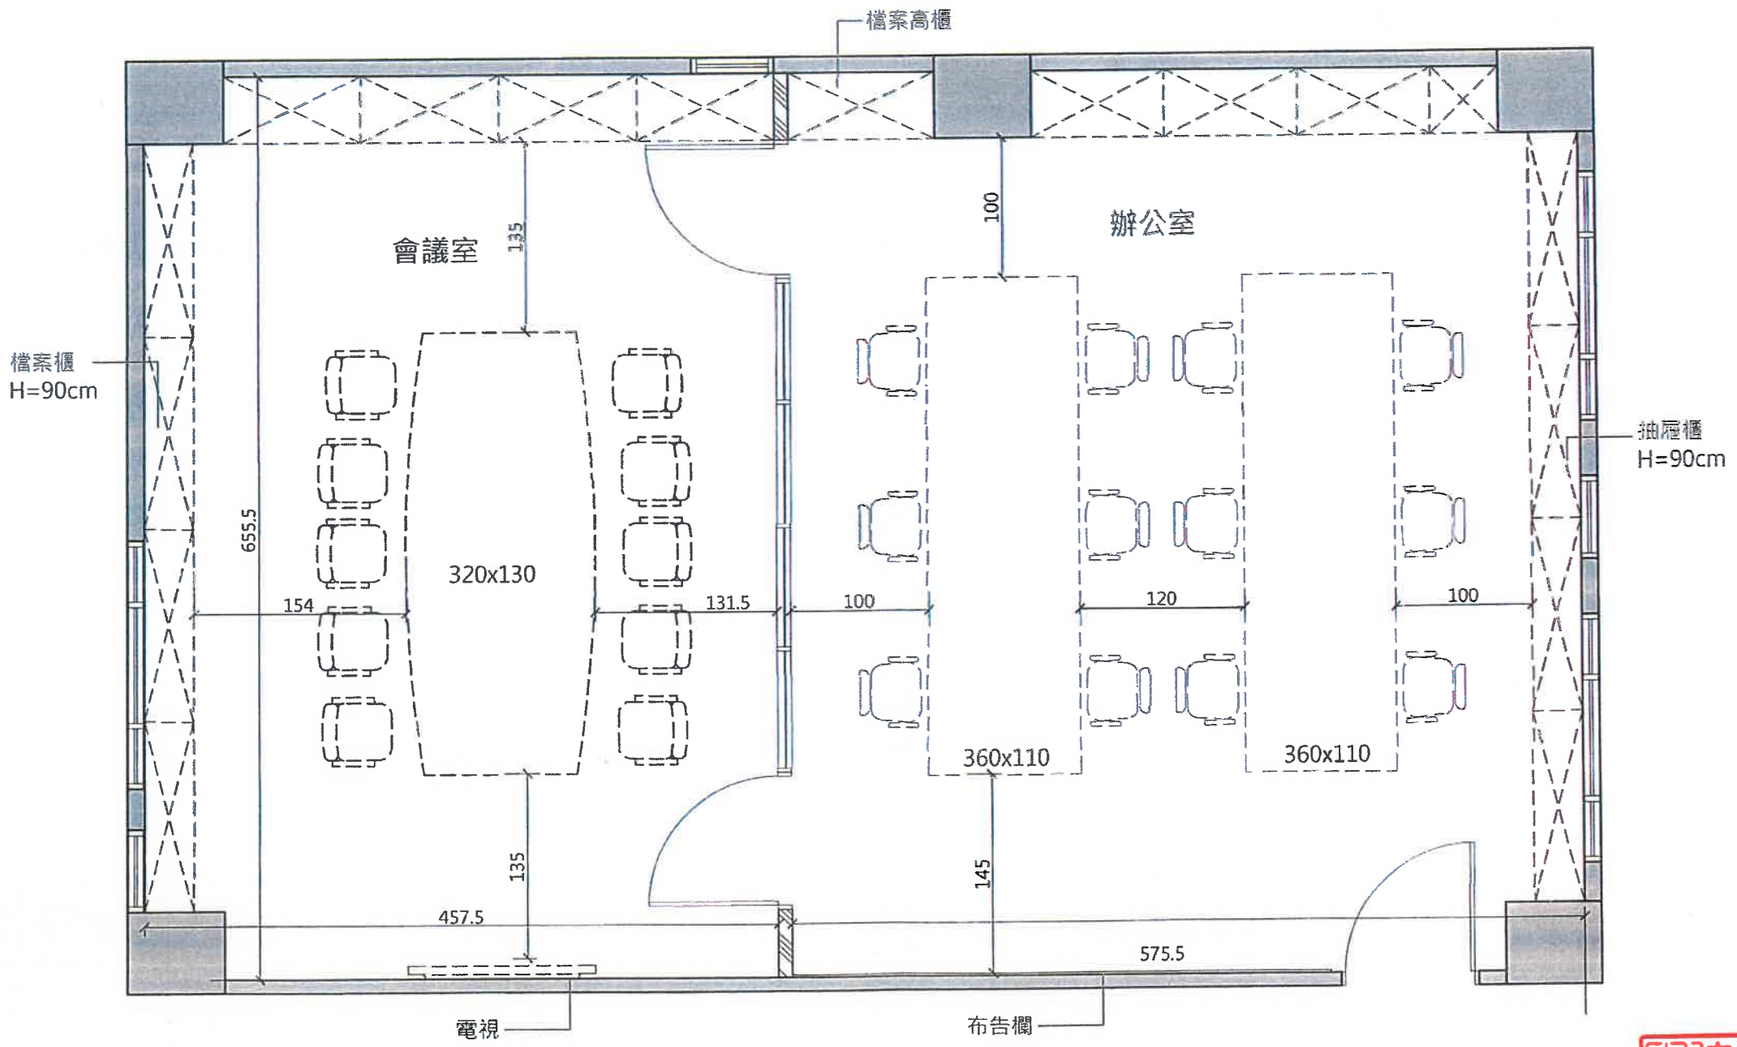


1 清潔隊辦公室平面圖 S=1/40

曾瑞宏

張號	
圖名	工程名稱
瀛災豬郭劉峰徜頭城	新竹縣竹北市公所清潔隊工作場所改善工程
繪圖	
設計	
修正	
校對	
日期	2025-06-30

尚強技術顧問有限公司
台中沙鹿區台灣大道六段1059號

比例尺	
圖號	A2-15

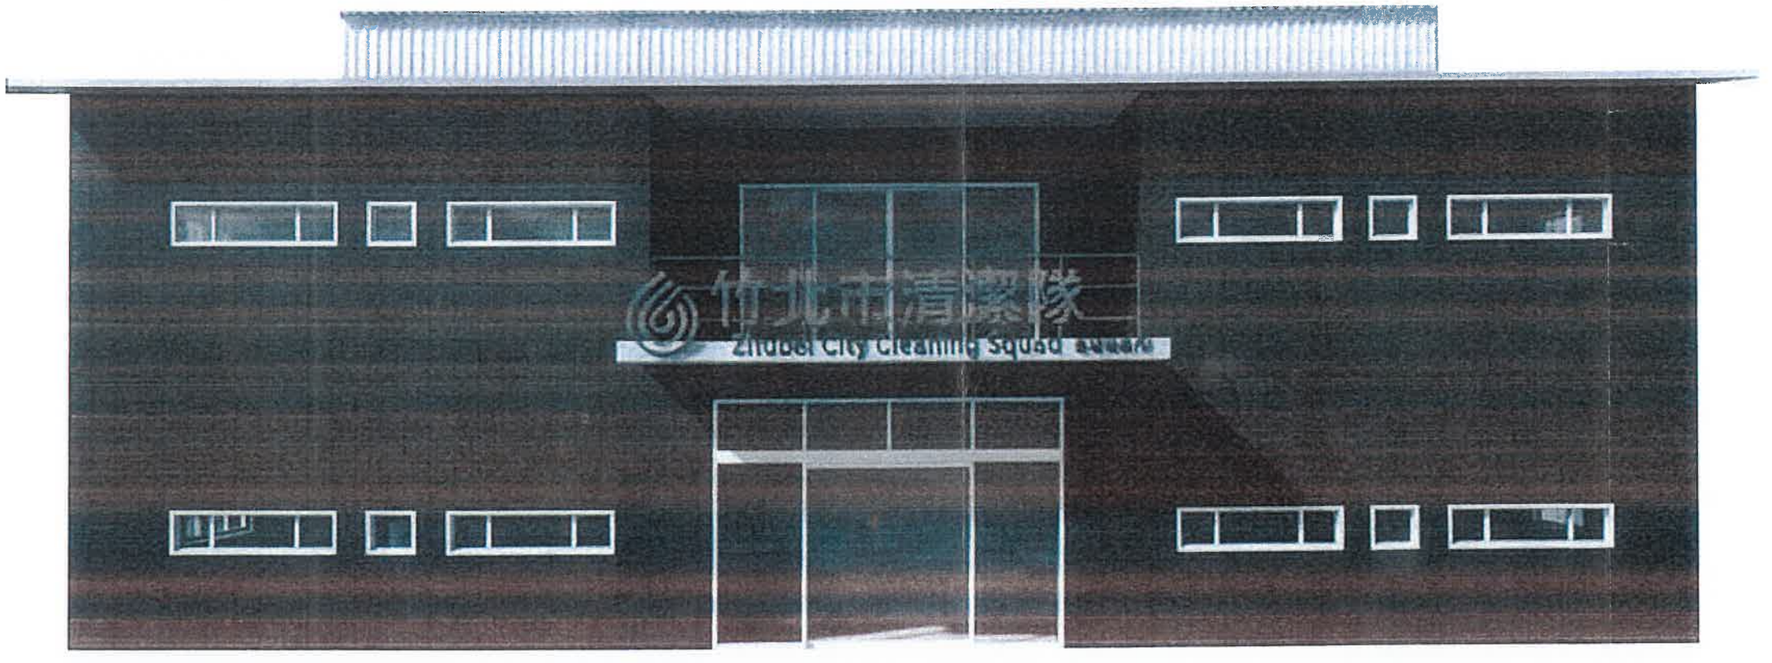


金屬外牆彩鋼漆

曾瑞宏


張　號	
圖　名	戶外立面圖
工程名稱	新竹縣竹北市公所清潔隊工作場所改善工程
繪　圖	
設　計	
修　正	
校　對	
日　期	2025-06-30

尚強技術顧問有限公司
台中沙鹿區台灣大道六段1069號

比例尺	
圖　號	A2-16

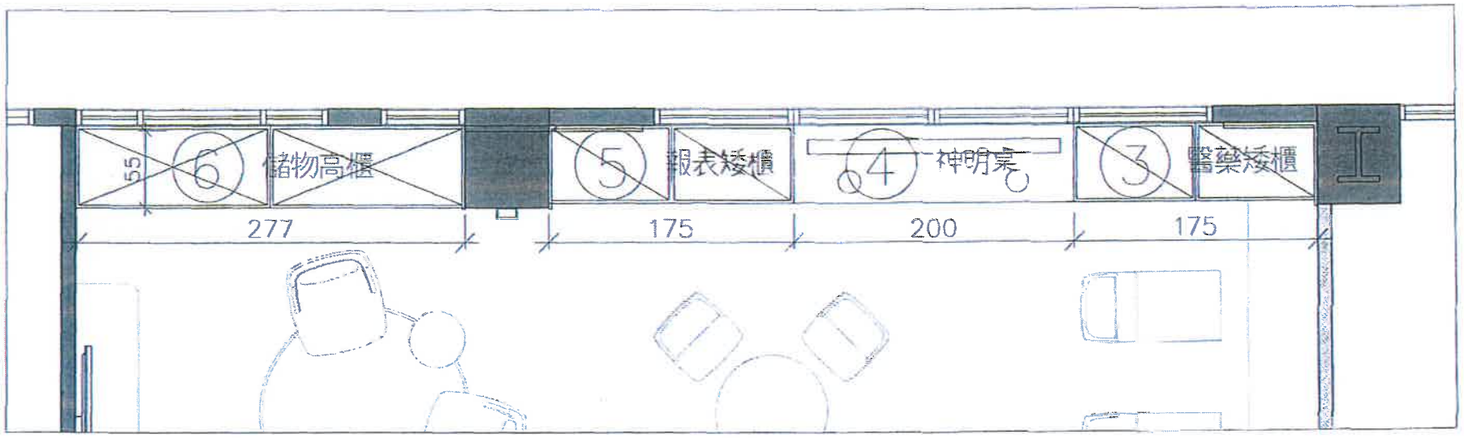


⑥ 儲物高櫃立面圖
SCALE 1/40

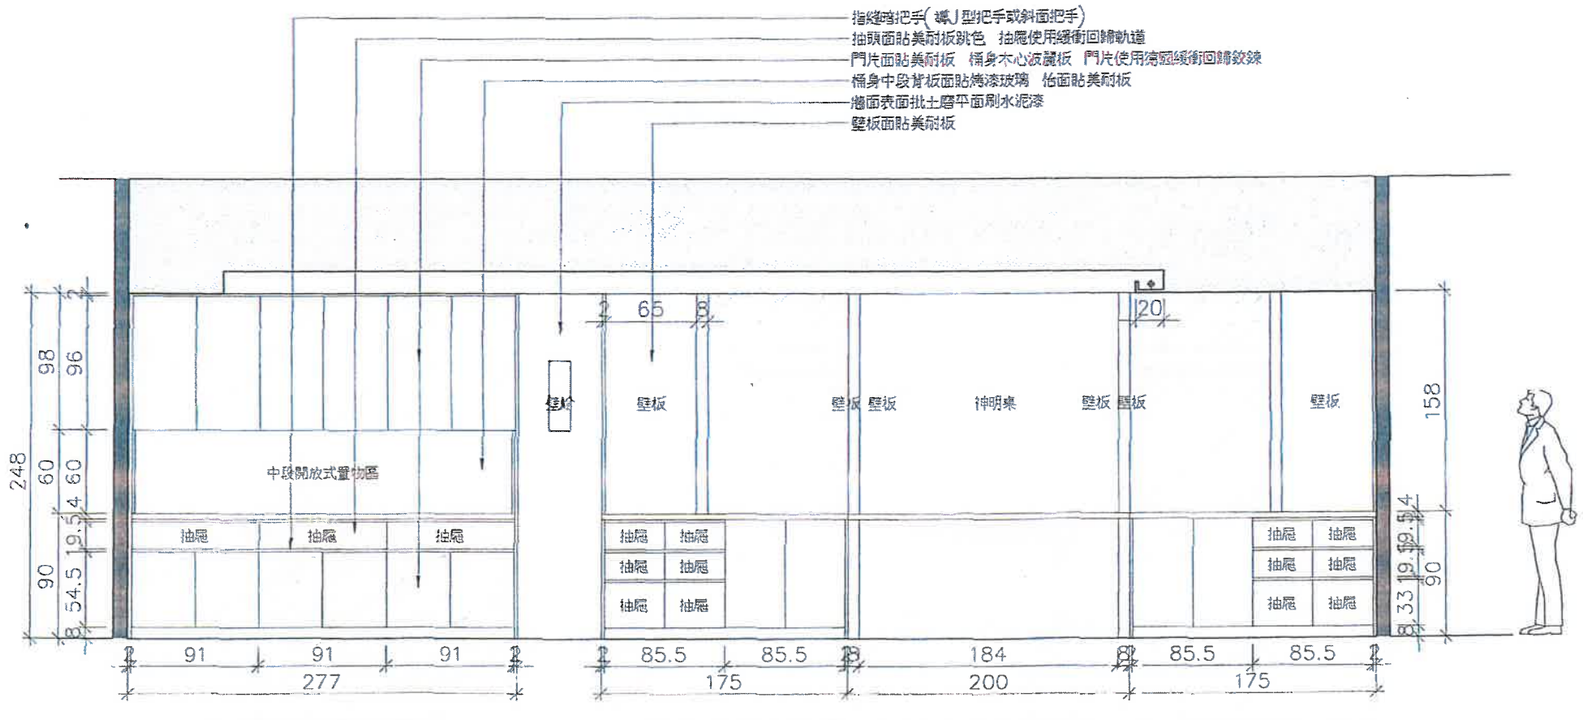

⑤ 報表矮櫃立面圖
SCALE 1/40

④ 神明桌立面圖
SCALE 1/40

③ 醫藥矮櫃立面圖
SCALE 1/40

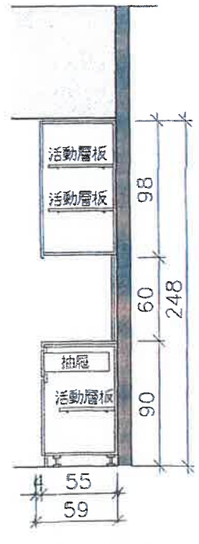


⑥ 剖立面圖
SCALE 1/40

張號	
圖名	工程名稱
木作詳圖1	新竹縣竹北市公所清潔隊工作場所改善工程
繪圖	
設計	
修正	
校對	
日期	2025-06-30


尚強技術顧問有限公司
台中沙鹿區台灣大道六段1059號

比例尺	
圖號	A3-01


宣瑞宏

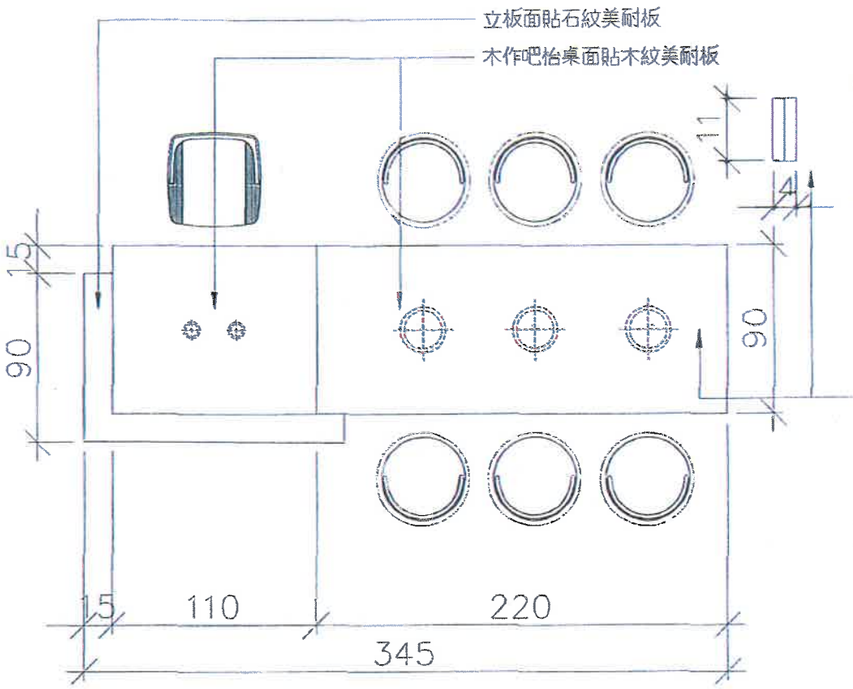


⑧ 迎賓吧枱整合餐桌平面圖 SCALE 1/30

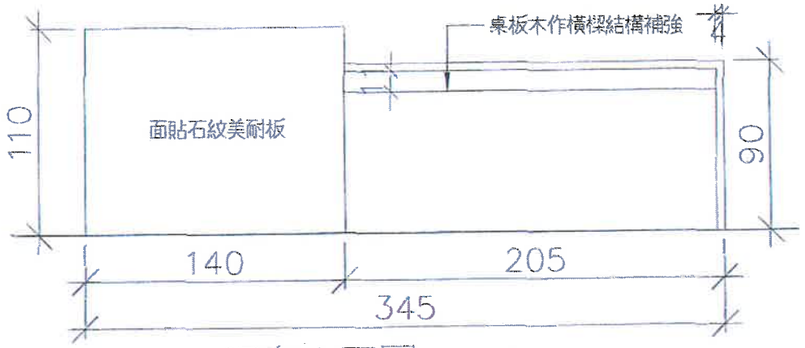


正向立面圖 S=1/30

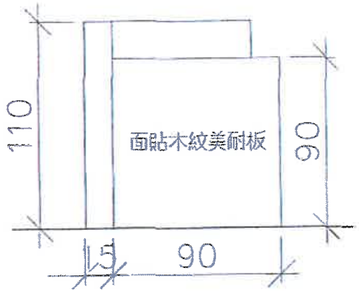


右側立面圖 S=1/30

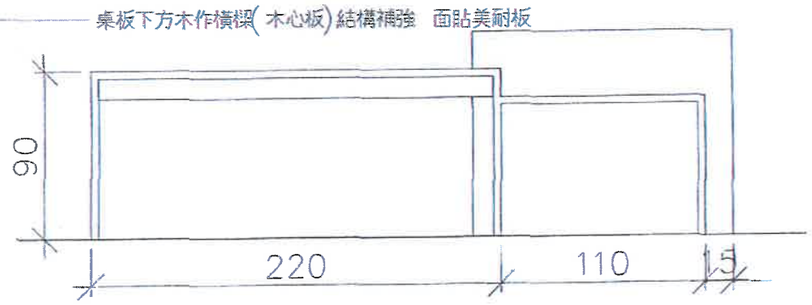


背向立面圖 S=1/30

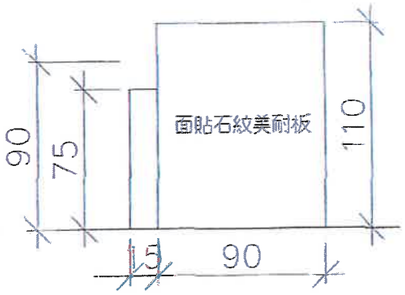


左側立面圖 S=1/30

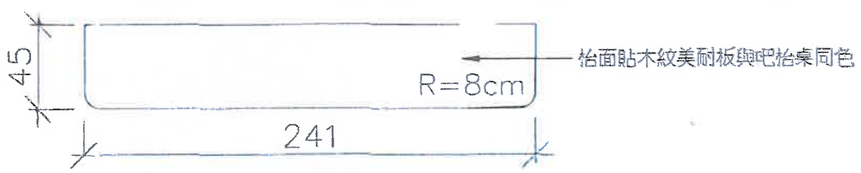

⑦ 電視矮櫃平面圖 SCALE 1/30

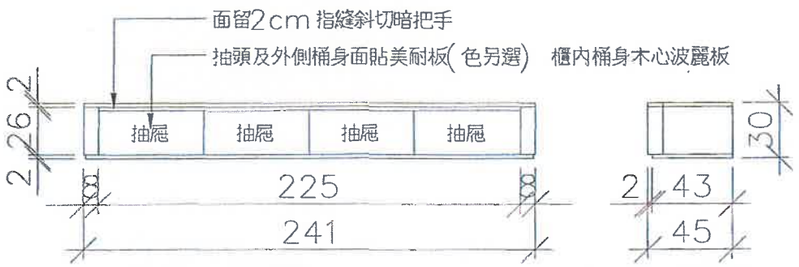

正向立面圖 S=1/30　　側向立面圖 S=1/30

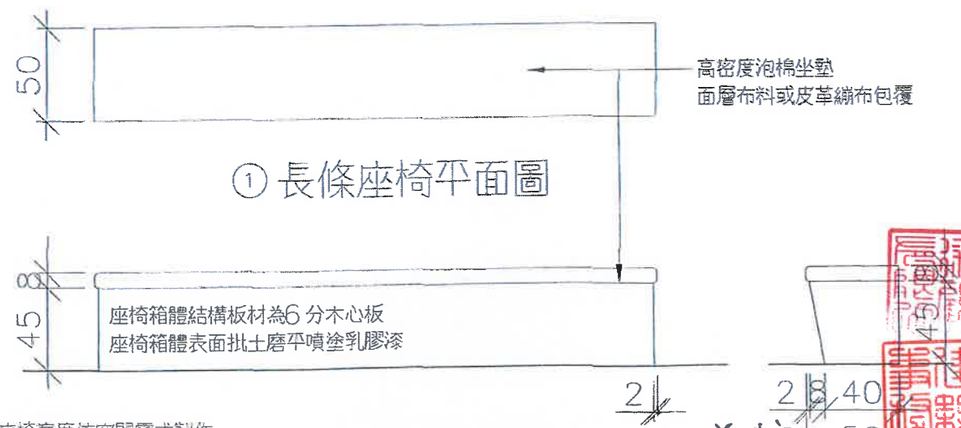


① 長條座椅平面圖


座椅寬度依空間需求製作
(大廳座椅W=750cm)
(廚房用餐區座椅W=416cm)
(女性休息區座椅共約W=736cm)


正向立面圖 S=1/30　　側向立面圖 S=1/30

張號	
圖名	木作詳圖2
工程名稱	新竹縣竹北市公所清潔隊工作場所改善工程
繪圖	
設計	
修正	
校對	
日期	2025-06-30
比例尺	
圖號	A3-02


尚強技術顧問有限公司
台中沙鹿區台灣大道六段1059號

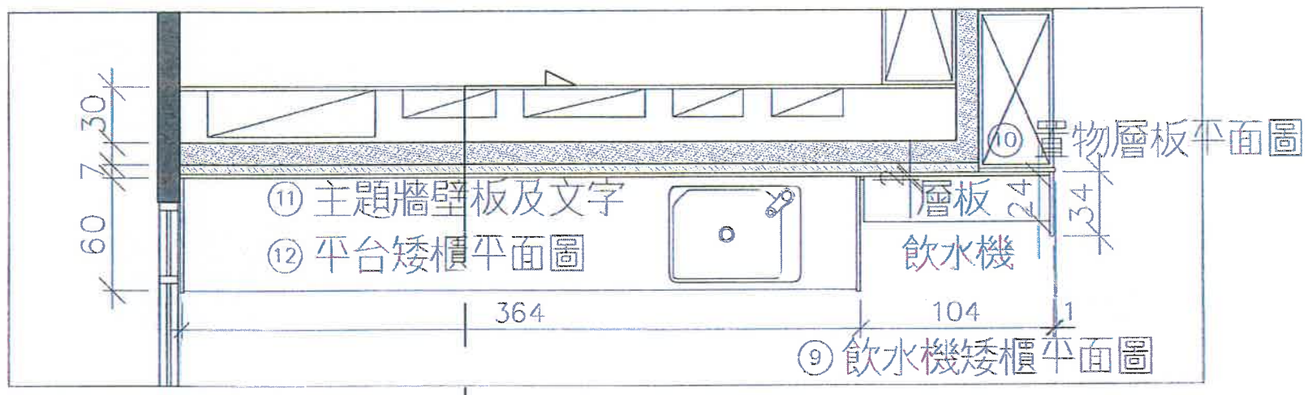

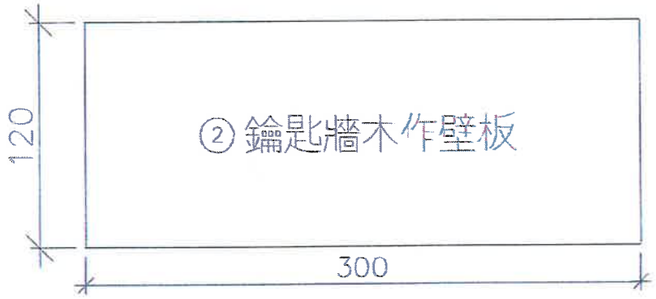

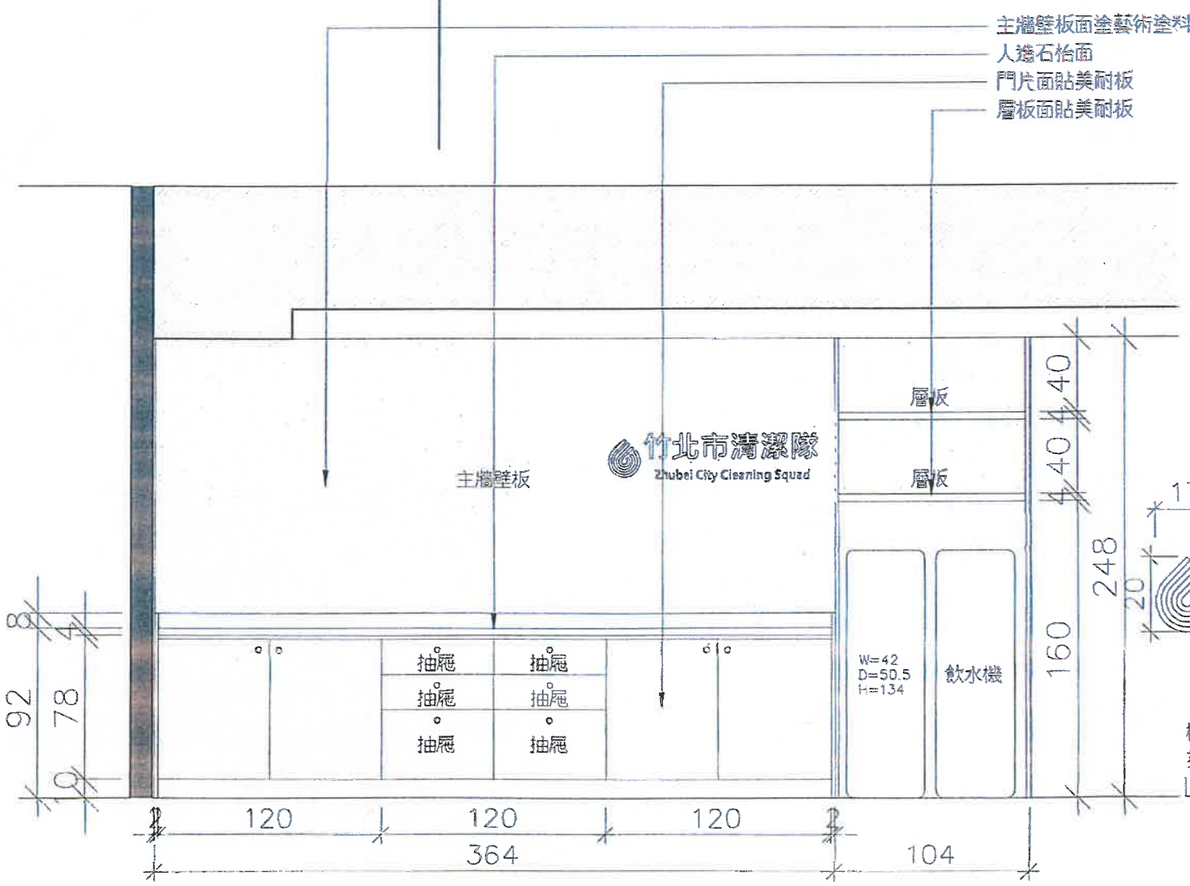

正向立面圖 S=1/30

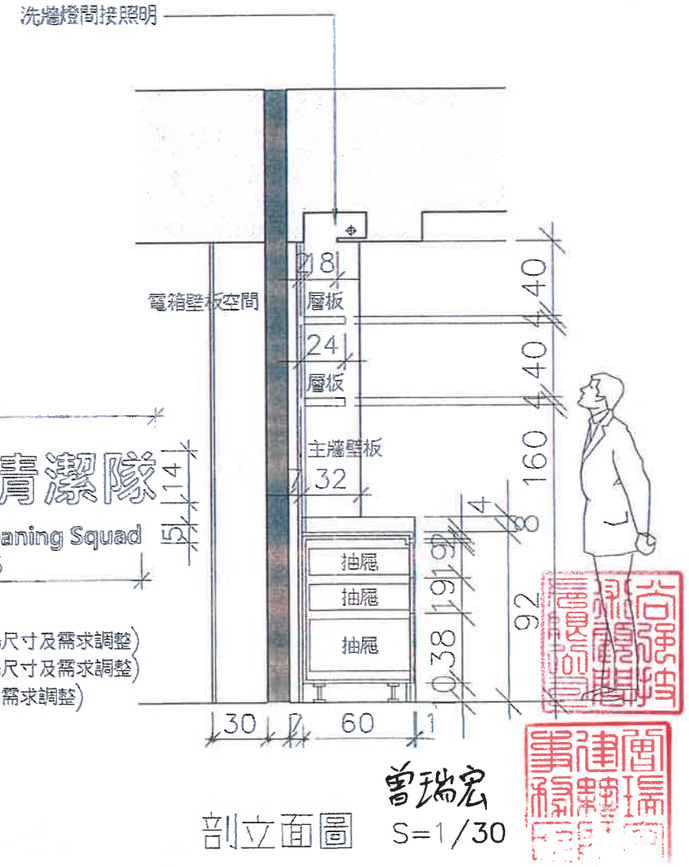

剖立面圖 S=1/30

曾瑞宏


張號	
圖名	工程名稱
木作詳圖3	新竹縣竹北市公所清潔隊工作場所改善工程
繪圖	
設計	
修正	
校對	
日期	2025-06-30

尚強技術顧問有限公司


台中沙鹿區台灣大道六段1059號

比例尺


圖號 A3-03

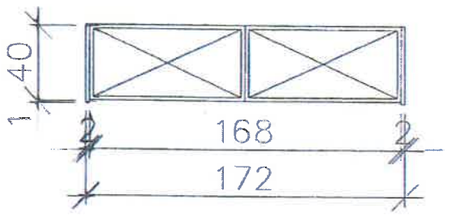


⑬ 走廊儲物高櫃平面圖 SCALE 1/30

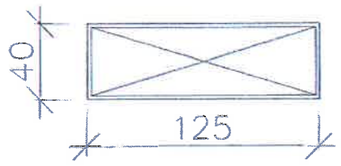


⑭ 車管室儲物高櫃平面圖 SCALE 1/30

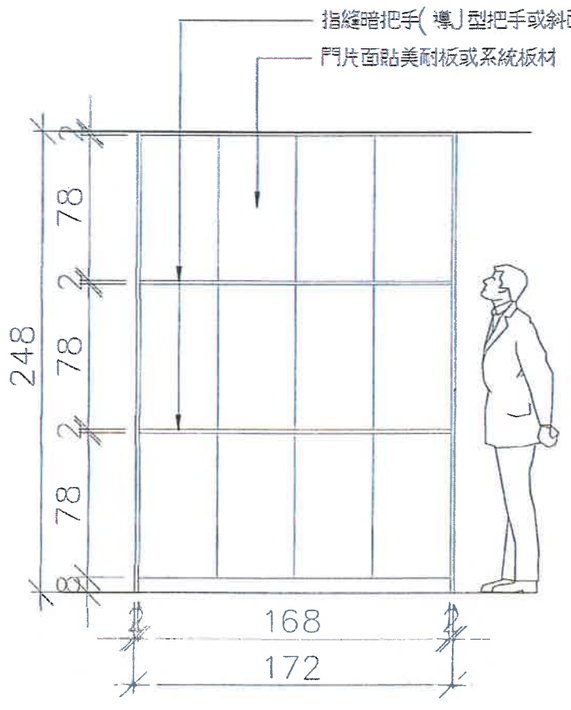


外側立面圖 S=1/30

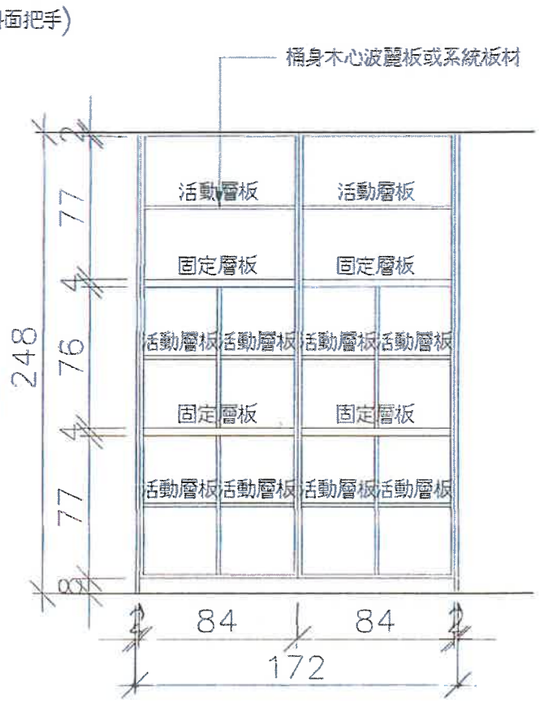

內部立面圖 S=1/30

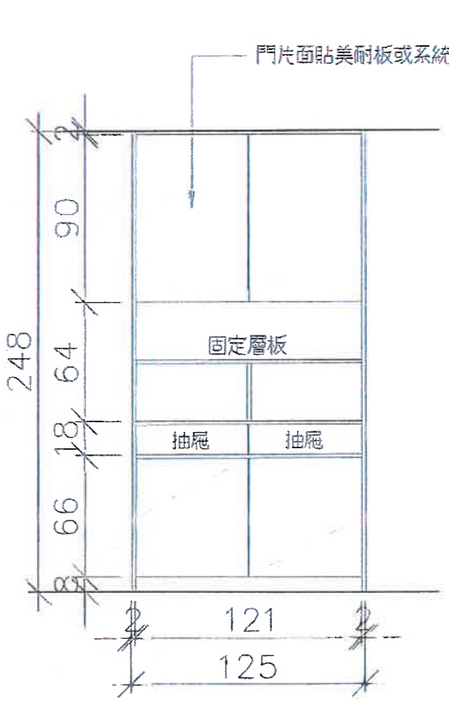

外側立面圖 S=1/30

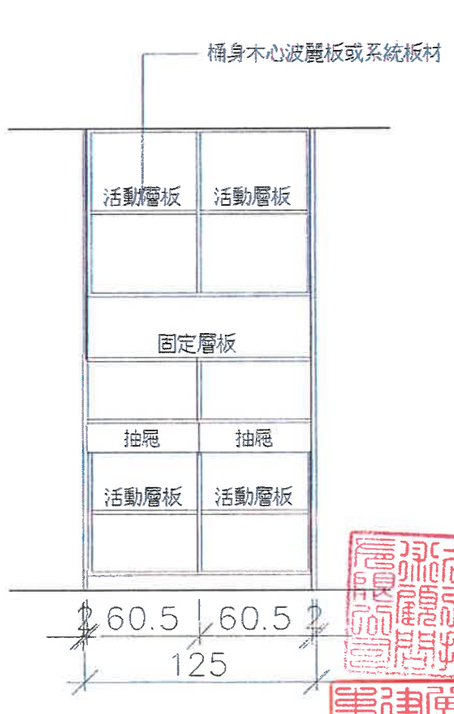


內部立面圖 S=1/30

曾瑞宏


張號	
圖名	木作詳圖4
工程名稱	新竹縣竹北市公所清潔隊工作場所改善工程
繪圖	
設計	
修正	
校對	
日期	2025-06-30

尚強技術顧問有限公司
台中沙鹿區台灣大道六段1059號

比例尺	
圖號	A3-04

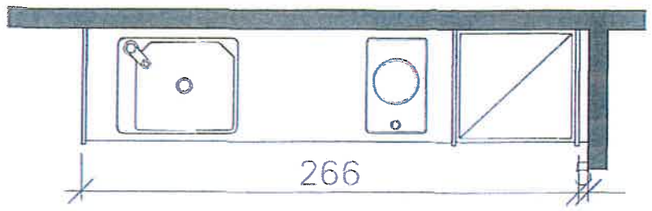


⑰ 廚房廚具矮櫃平面圖
SCALE 1/30

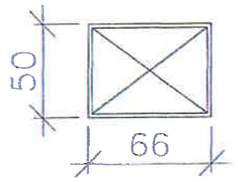


⑱ 儲物高櫃平面圖
SCALE 1/30


⑯ 廚房電器高櫃平面圖
SCALE 1/30

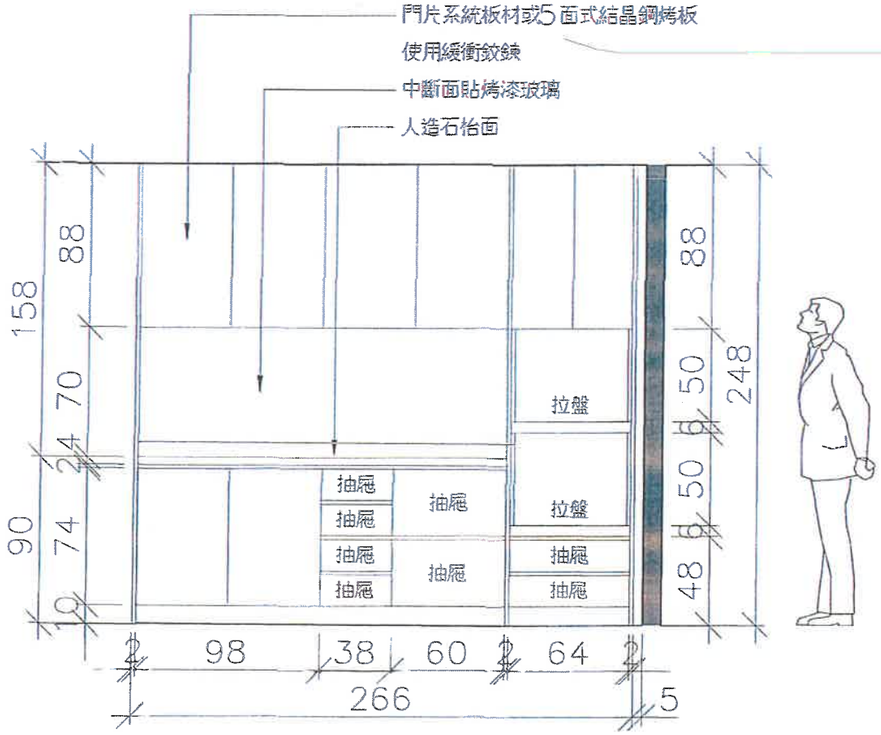

正向立面圖 S=1/30

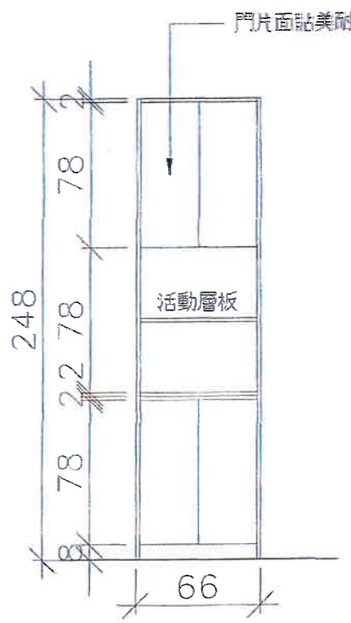

外側立面圖 S=1/30

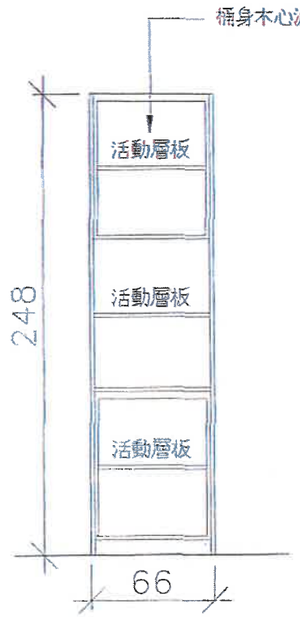

內部立面圖 S=1/30

曾瑞宏

張號

圖名 工程名稱

木作詳圖5

新竹縣竹北市公所清潔隊
工作場所改善工程

繪圖

設計

修正


校對

日期
2025-06-30


尚強技術顧問有限公司
台中沙鹿區台灣大道六段1059號

比例尺


A3-05

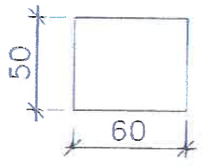


⑲個人置物高櫃平面圖
SCALE 1/30

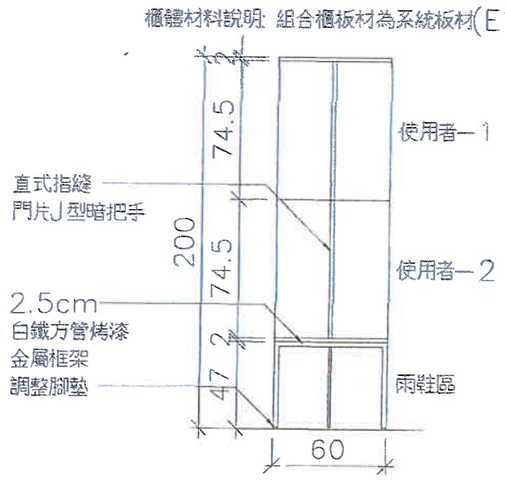


外側立面圖 S=1/30

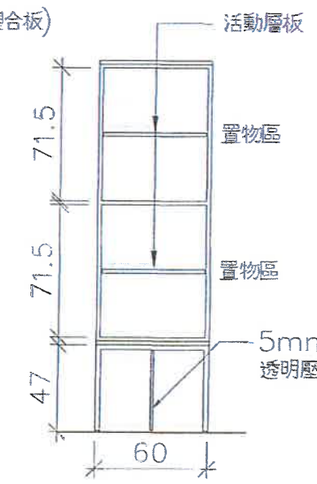

內部立面圖 S=1/30

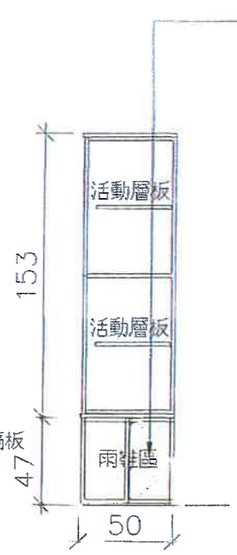

剖立面圖 S=1/30

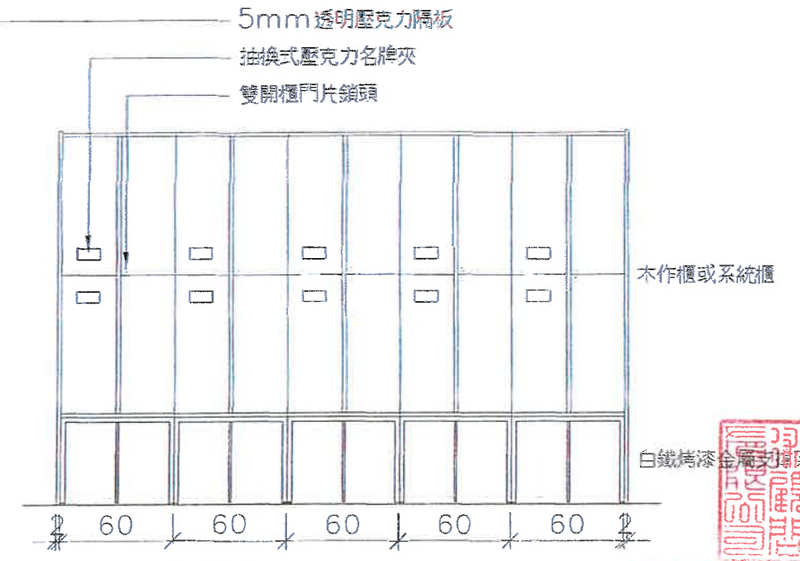


女櫃組合示意圖 S=1/30


張號	
圖名	木作詳圖6
工程名稱	新竹縣竹北市公所清潔隊工作場所改善工程
繪圖	
設計	
修正	
校對	
日期	2025-06-30

尚強技術顧問有限公司
台中沙鹿區台灣大道六段1059號


比例尺	
圖號	A3-06

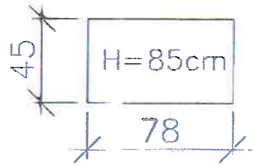


㉑ 平台平面圖 SCALE 1/30

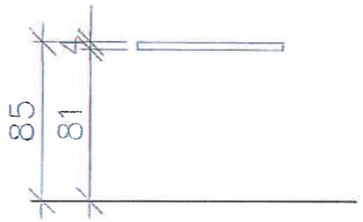


正向立面圖

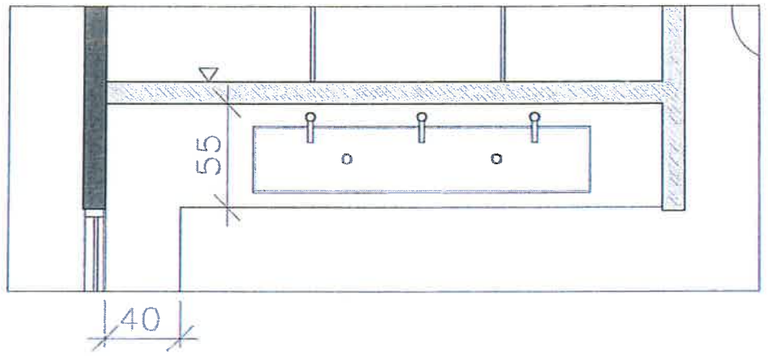


⑳ 洗手枱及枱下矮櫃平面圖
SCALE 1/30

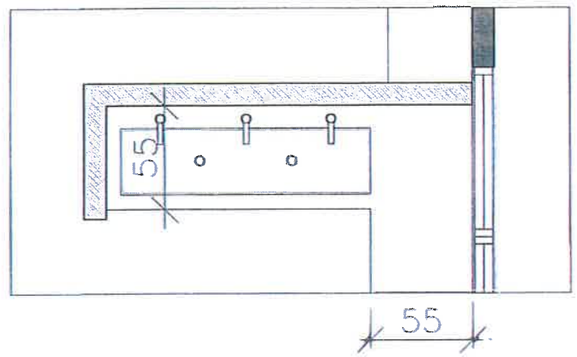


⑳ 洗手枱及枱下矮櫃平面圖
SCALE 1/30

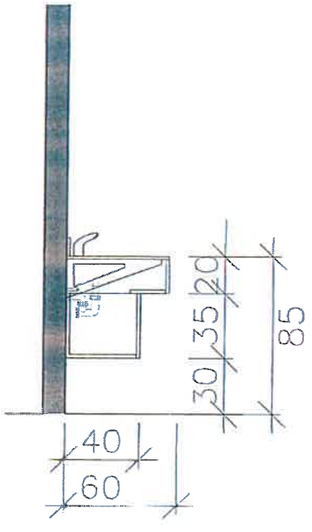

剖立面圖 S=1/30

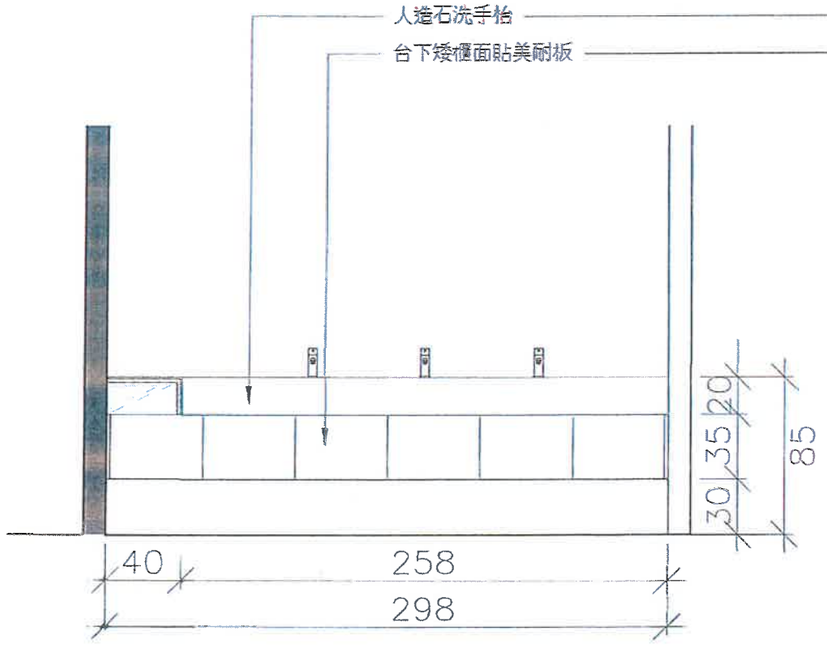

正向立面圖 S=1/30

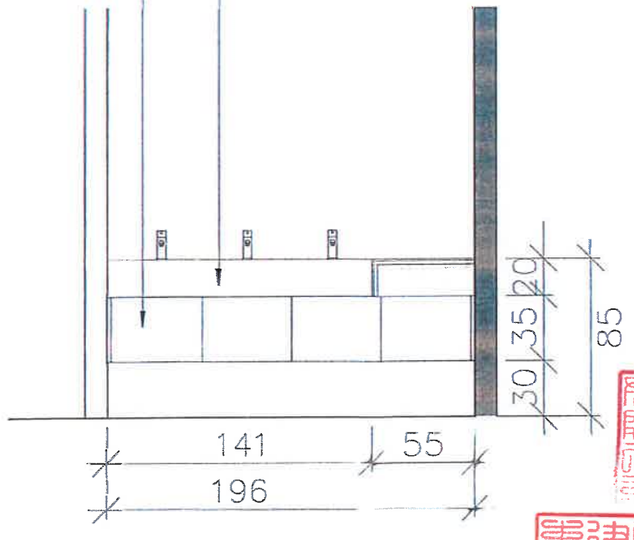


正向立面圖 S=1/30

曾瑞宏

張號	
圖名	木作詳圖7
工程名稱	新竹縣竹北市公所清潔隊工作場所改善工程
繪圖	
設計	
修正	
校對	
日期	2025-06-30


尚強技術顧問有限公司
台中沙鹿區台灣大道六段1059號

比例尺	
圖號	A3-07

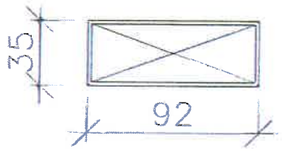

㉓ 掃具高櫃平面圖

SCALE 1/30

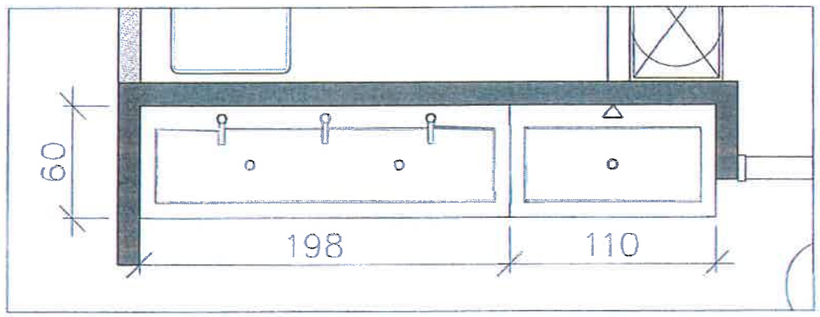

㉒ 洗手枱及枱下矮櫃平面圖

SCALE 1/30

外側立面圖 S=1/30　內部立面圖 S=1/30　剖立面圖 S=1/30　正向立面圖 S=1/30　剖立面圖 S=1/30

曾瑞宏


張號	
圖名	工程名稱
木作詳圖8	新竹縣竹北市公所清潔隊工作場所改善工程
繪圖	
設計	
修正	
校對	
日期	2025-06-30

尚強技術顧問有限公司


台中沙鹿區台灣大道六段1059號

比例尺


圖號 A3-08

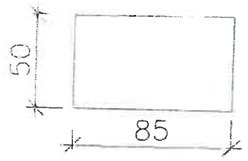


㉔個人置物高櫃平面圖
SCALE 1/30

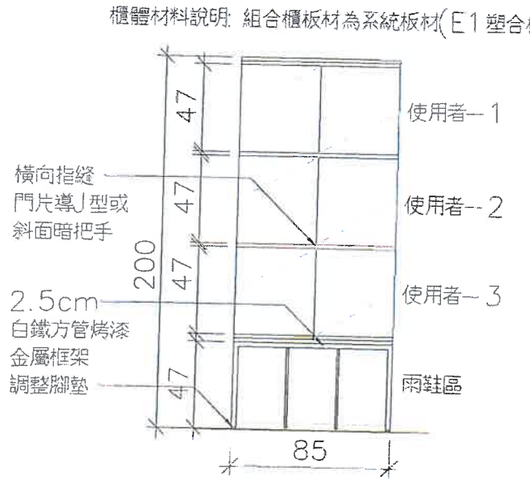


外側立面圖 S=1/30

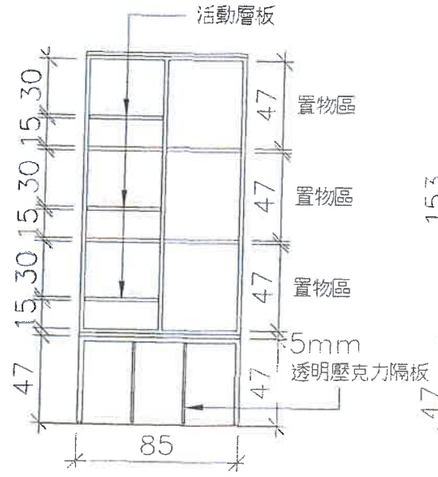

內部立面圖 S=1/30

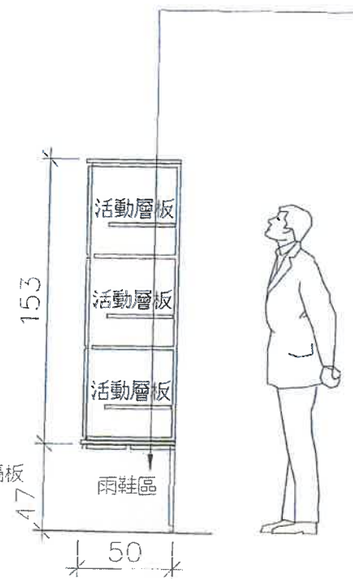

剖立面圖 S=1/30

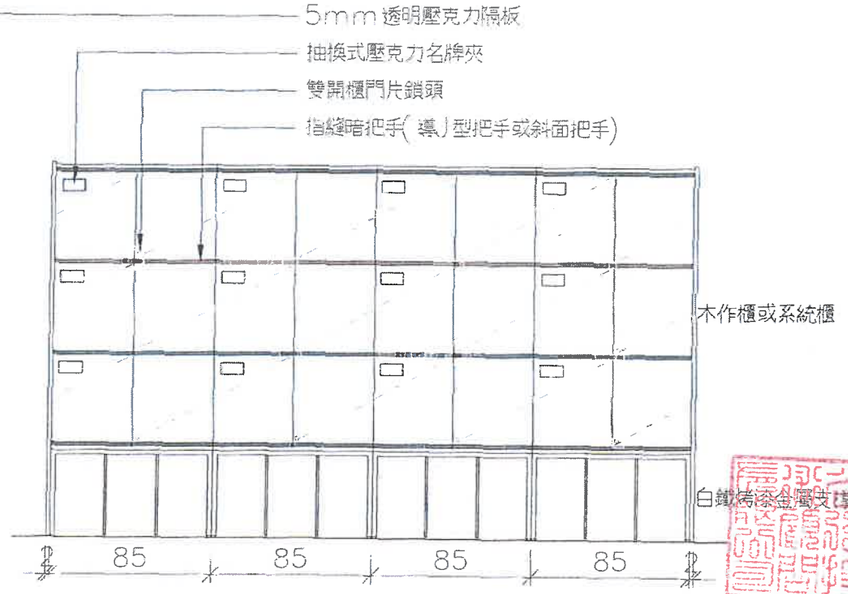


男櫃組合示意圖 S=1/30

曾瑞宏


張號	
圖名	木作詳圖9
工程名稱	新竹縣竹北市公所清潔隊工作場所改善工程
繪圖	
設計	
修正	
校對	
日期	2025-06-30

尚強技術顧問有限公司
台中沙鹿區台灣大道六段1050號


比例尺	
圖號	A3-09

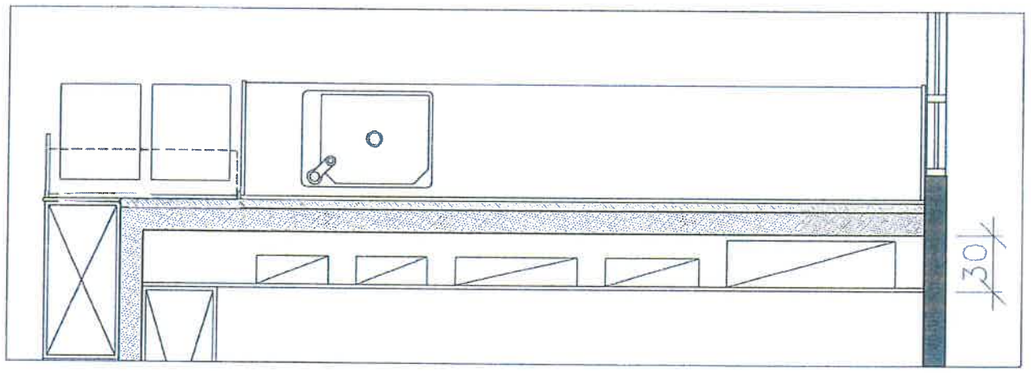


⑮ 車管室電箱壁板牆平面圖
SCALE 1/30

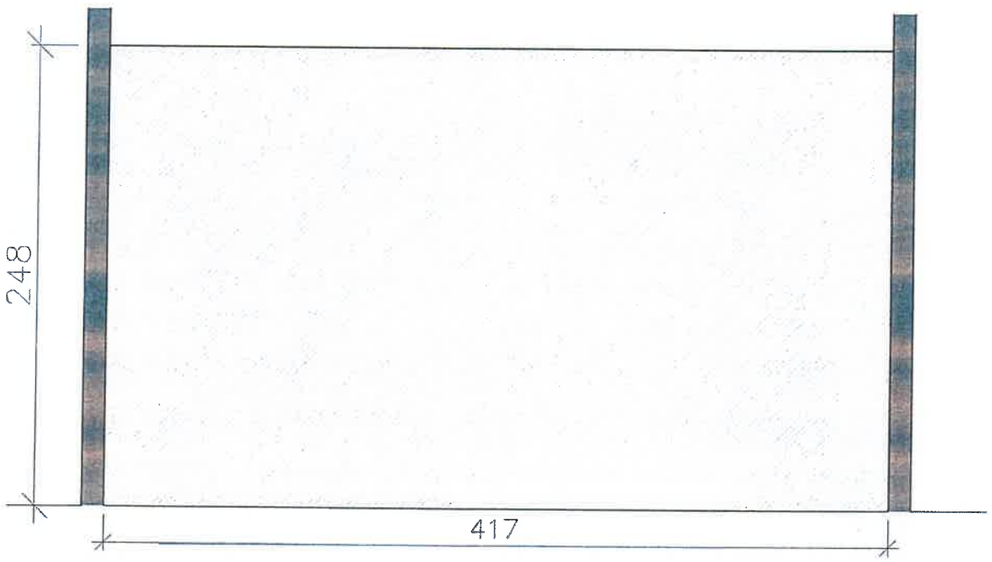

正向立面圖 S=1/30

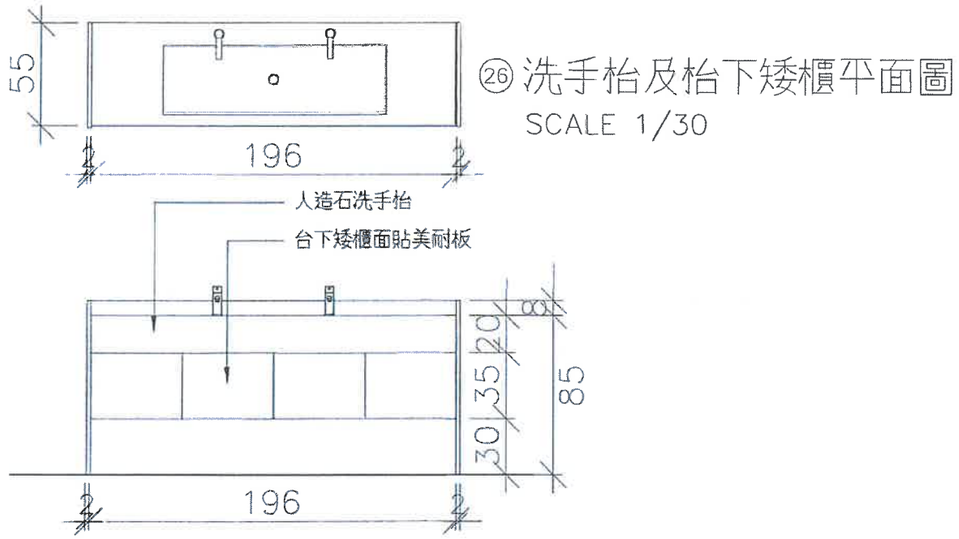

㉖ 洗手枱及枱下矮櫃平面圖
SCALE 1/30

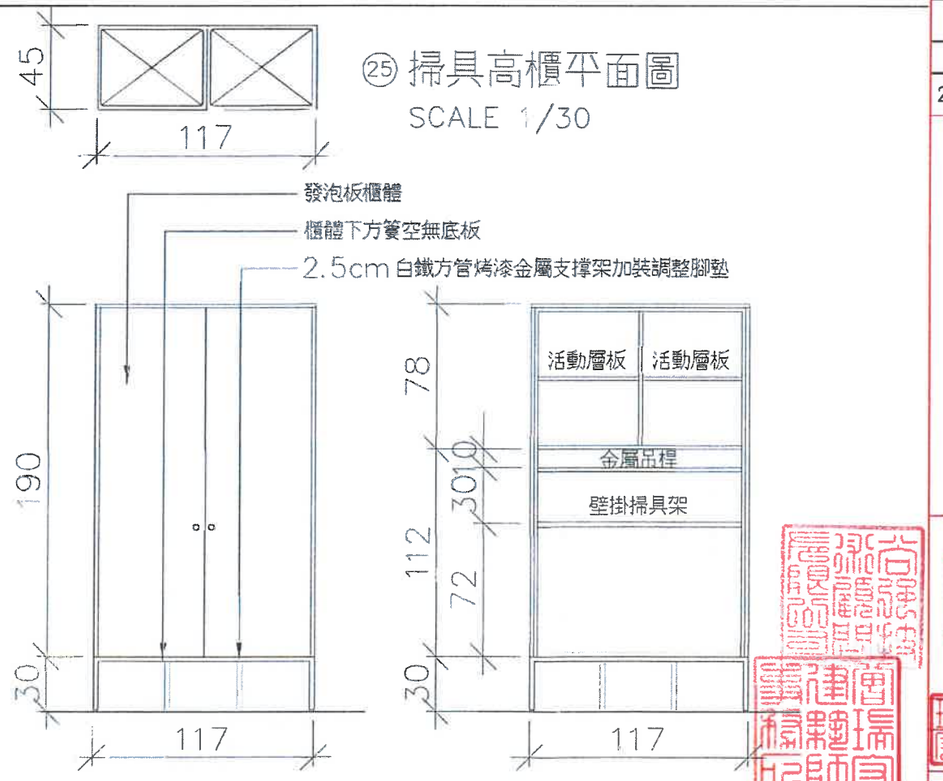

㉕ 掃具高櫃平面圖
SCALE 1/30

外側立面圖 S=1/30


內部立面圖 S=1/30

曾瑞宏

張號	
圖名	工程名稱
木作詳圖 10	新竹縣竹北市公所清潔隊工作場所改善工程
繪圖	
設計	
修正	
校對	
日期	2025-06-30


尚強技術顧問有限公司
台中沙鹿區台灣大道六段1059號

比例尺	
圖號	A3-10

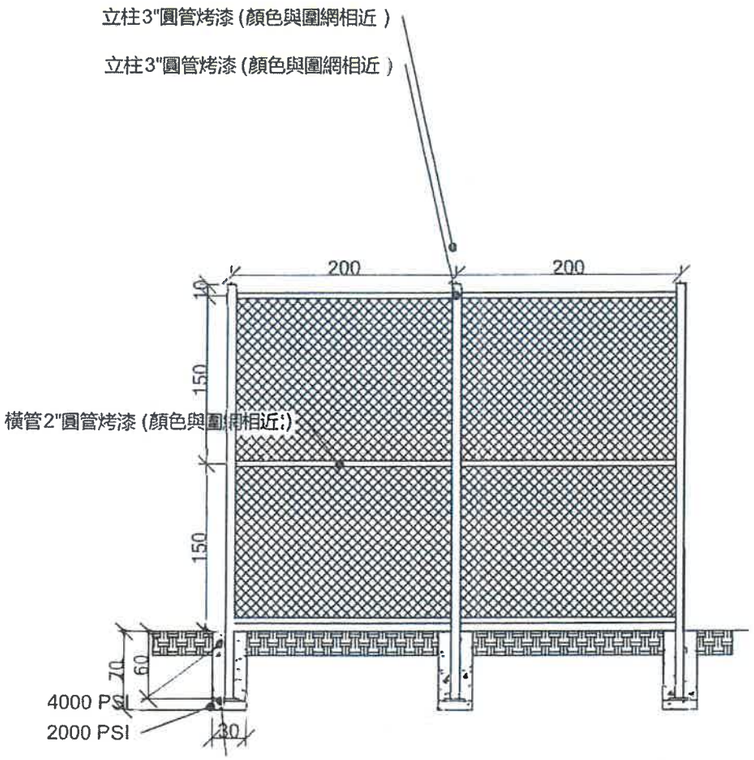


焊接20cm方形鋼板 t:2mm

1/50 圍欄基礎剖面圖

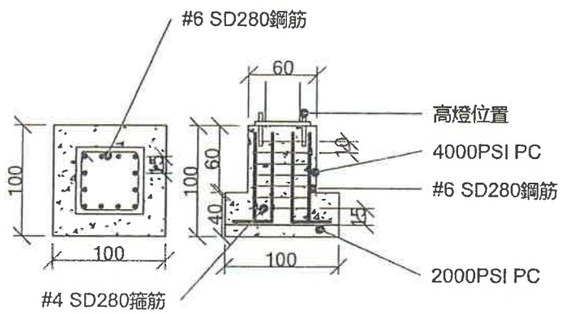

1/50 高燈基礎圖

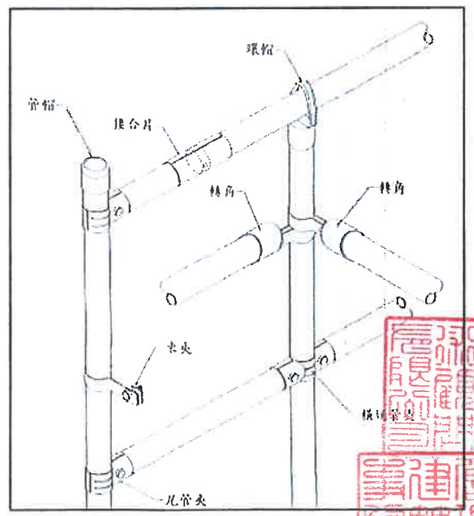


相關五金零件示意圖
S: 1/50

張號	
圖名	工程名稱
圍籬詳圖	新竹縣竹北市公所清潔隊工作場所改善工程
繪圖	
設計	
修正	
校對	
日期	2025-06-30


尚強技術顧問有限公司
台中沙鹿區台灣大道六段1059號

比例尺


圖號 A3-11

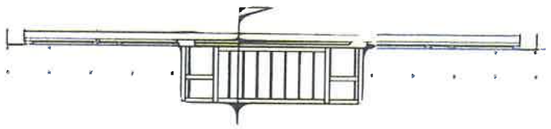


平面結構平面圖 SC:1/200

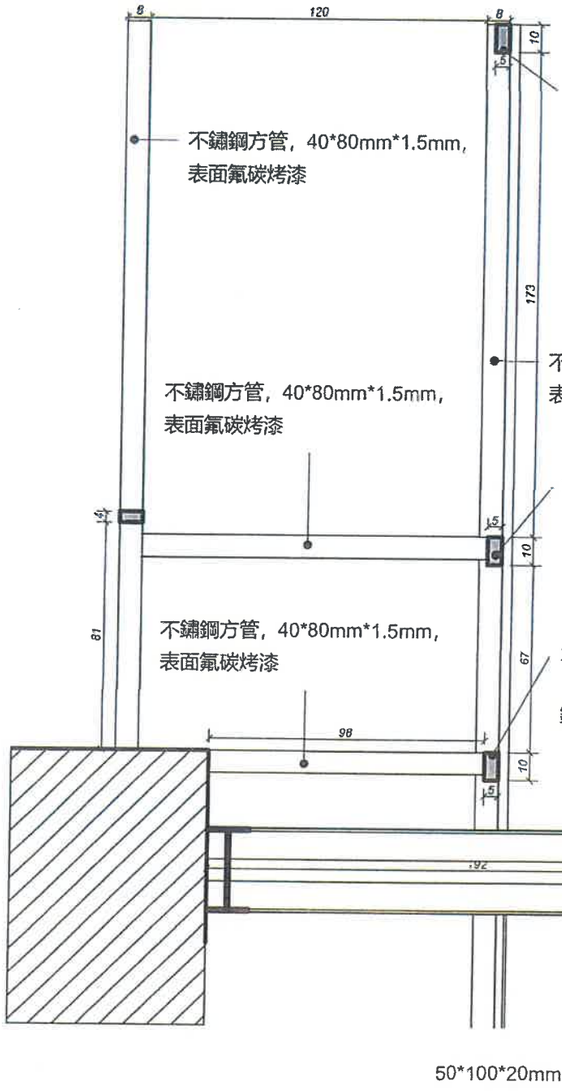

立面結構平面圖 SC:1/50

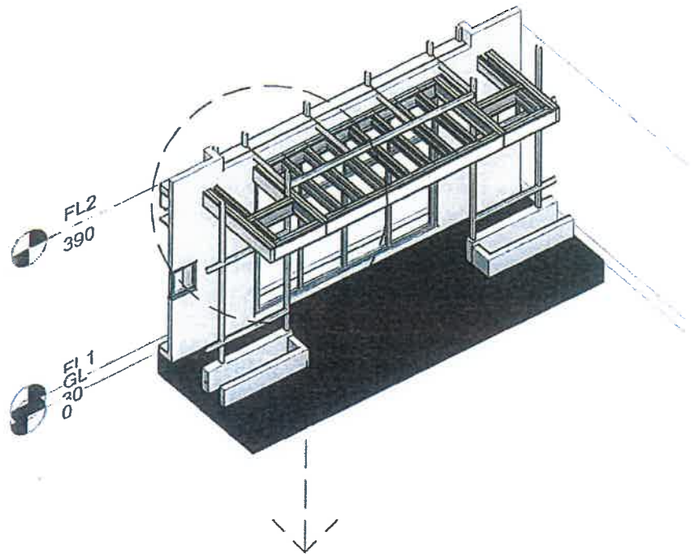

3D示意圖

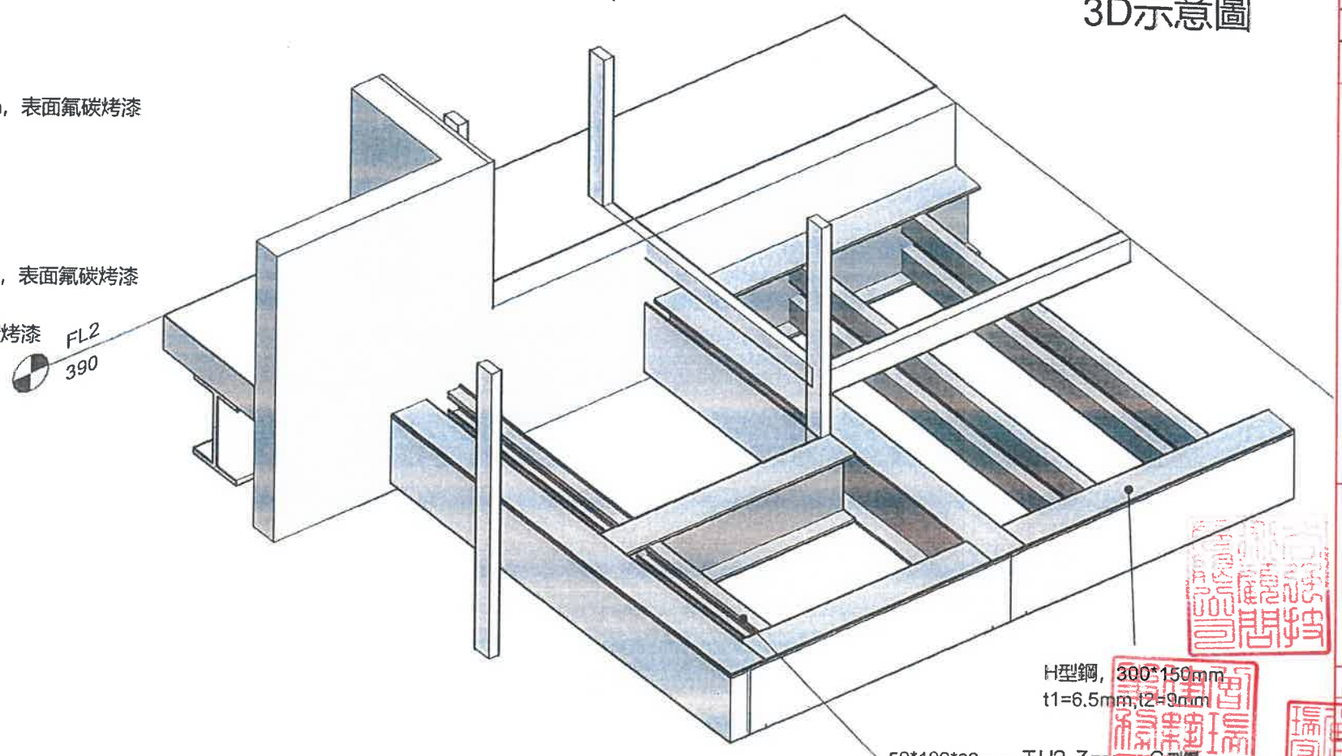


張　號	
圖　名	工程名稱
鋁包版入口雨遮	新竹縣竹北市公所清潔隊 工作場所改善工程
繪　圖	
設　計	
修　正	
校　對	
日　期	2025-06-30


尚強技術顧問有限公司
台中沙鹿區台灣大道六段1059號

比例尺	
圖　號	A3-12

曾瑞宏

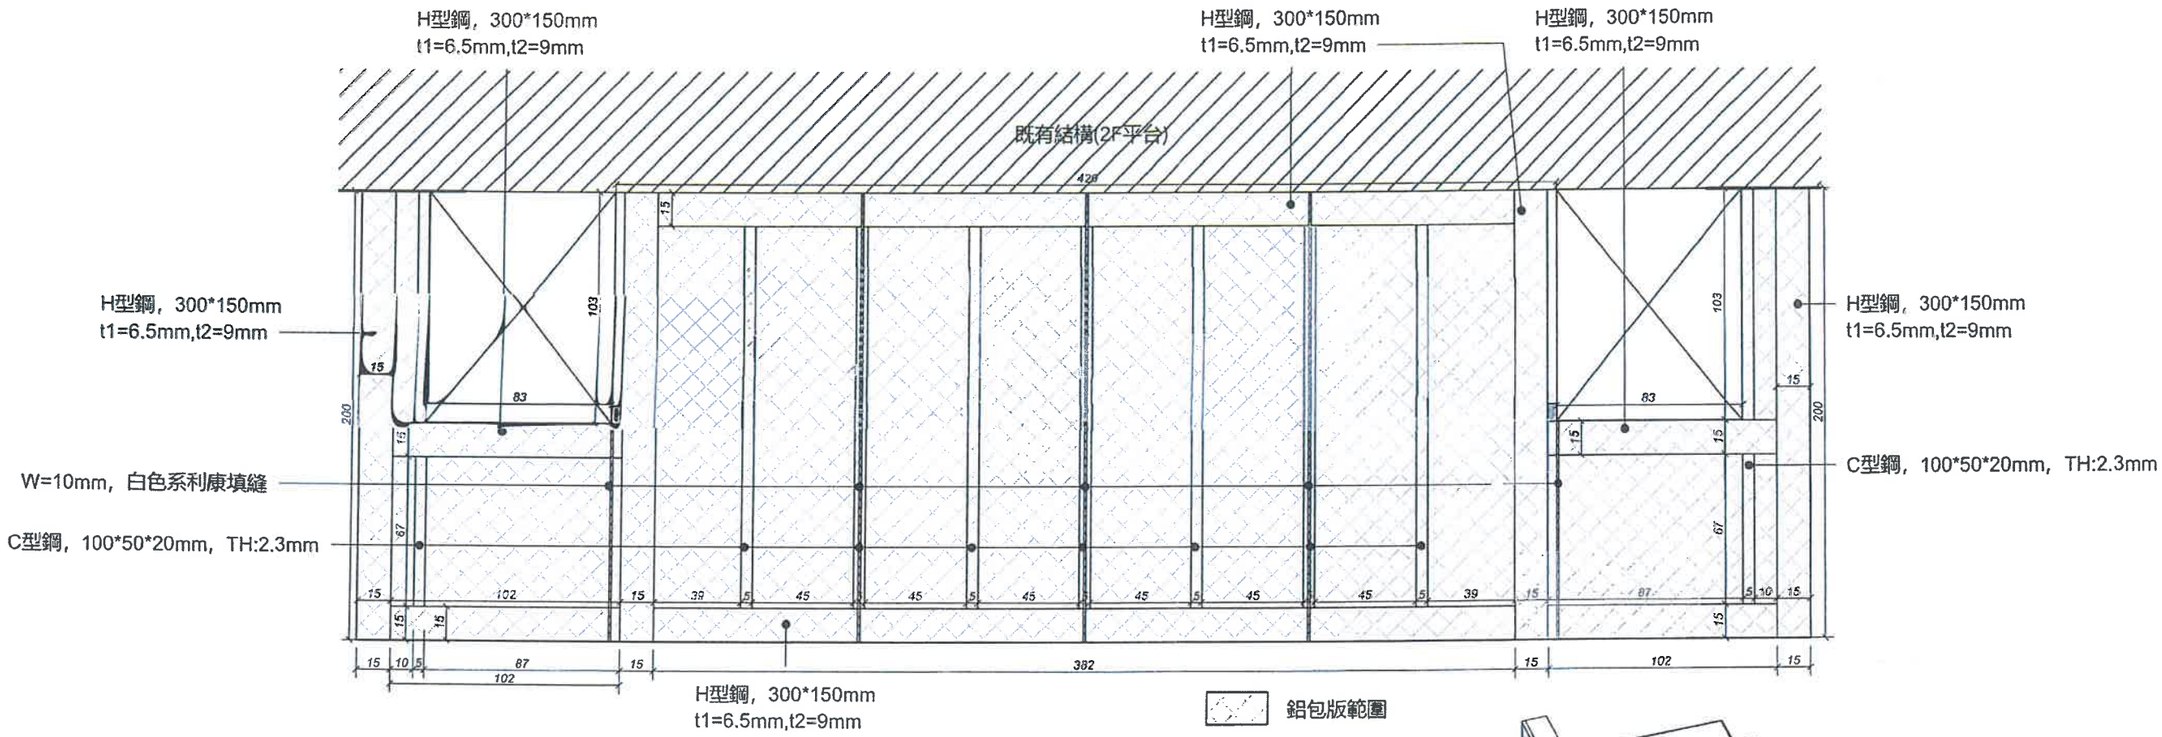

鋁包版結構圖 SC:1/25

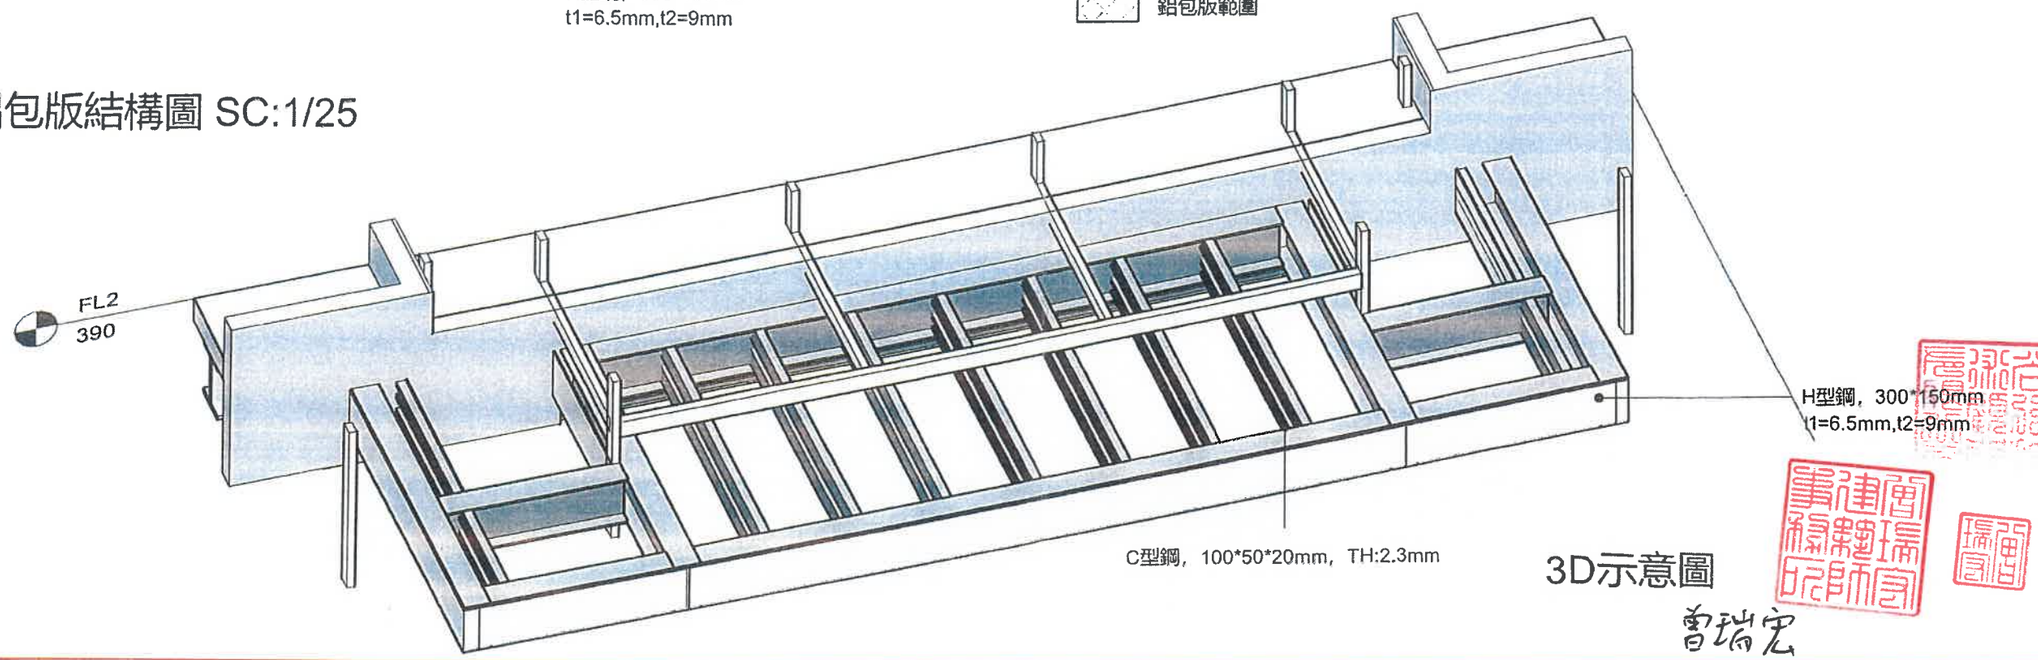


3D示意圖

曾瑞宏

張號	
圖名	雨遮詳圖
工程名稱	新竹縣竹北市公所清潔隊工作場所改善工程
繪圖	
設計	
修正	
校對	
日期	2025-06-30

尚強技術顧問有限公司
台中沙鹿區台灣大道六段1059號

比例尺	
圖號	A3-13

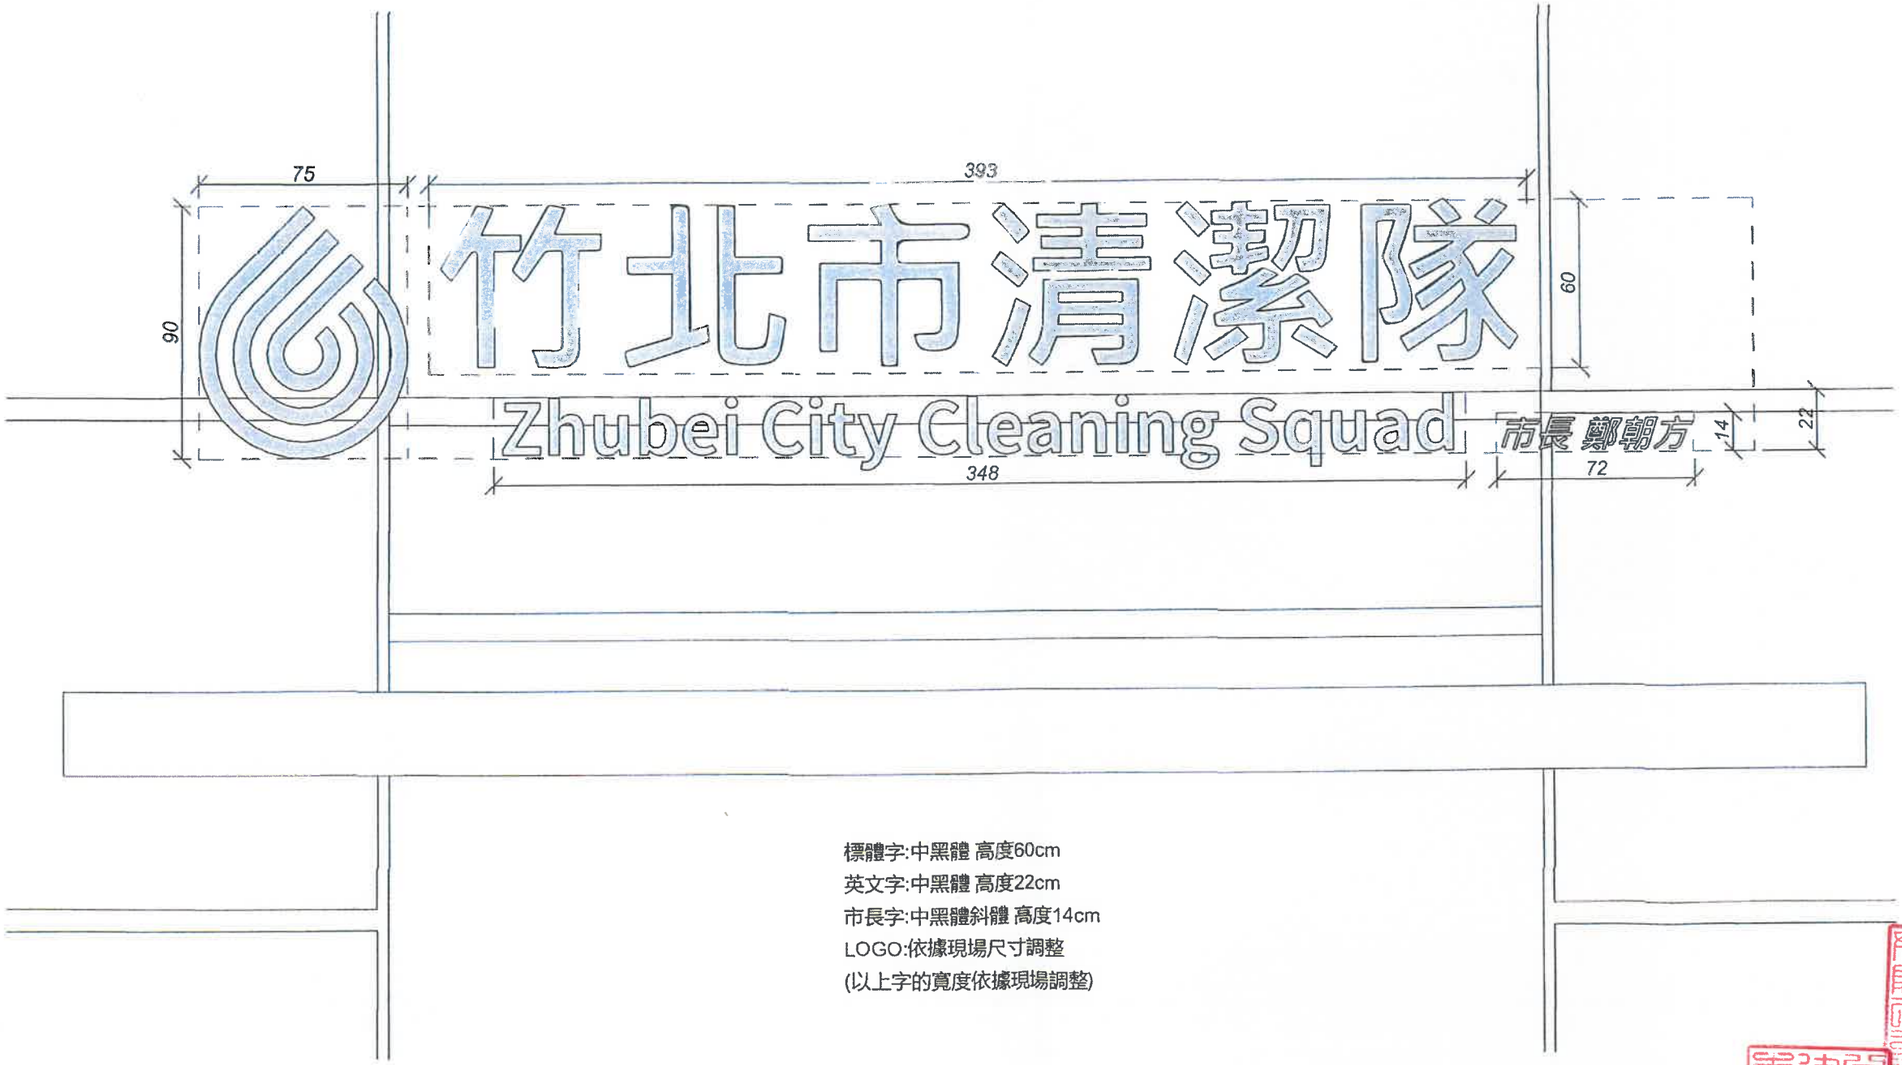

標體字:中黑體 高度60cm
英文字:中黑體 高度22cm
市長字:中黑體斜體 高度14cm
LOGO:依據現場尺寸調整
(以上字的寬度依據現場調整)

外觀立面招牌字尺寸圖 SC:1/20

張號	
圖名	工程名稱
外觀立面招牌尺寸圖	新竹縣竹北市公所清潔隊工作場所改善工程
繪圖	
設計	
修正	
校對	
日期	2025-06-30

尚強技術顧問有限公司
台中沙鹿區台灣大道六段1059號

比例尺	
圖號	A3-14

曾瑞宏